



PROJECT :

*PROPOSED 3(THREE) STORIED RESIDENTIAL BUILDING
FOR MD.SHOFIQUE AT AT CHAR VEDURIA,BANKERHAT,BHOLA,BANGLADESH.
KHATIAN NO:-4007,JL NO:-056,DAG NO:-2332,1888*


DATE: 25-01-2026

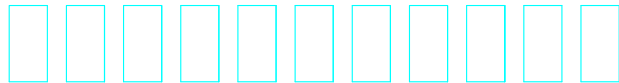

ARCHITECTURAL DRAWING

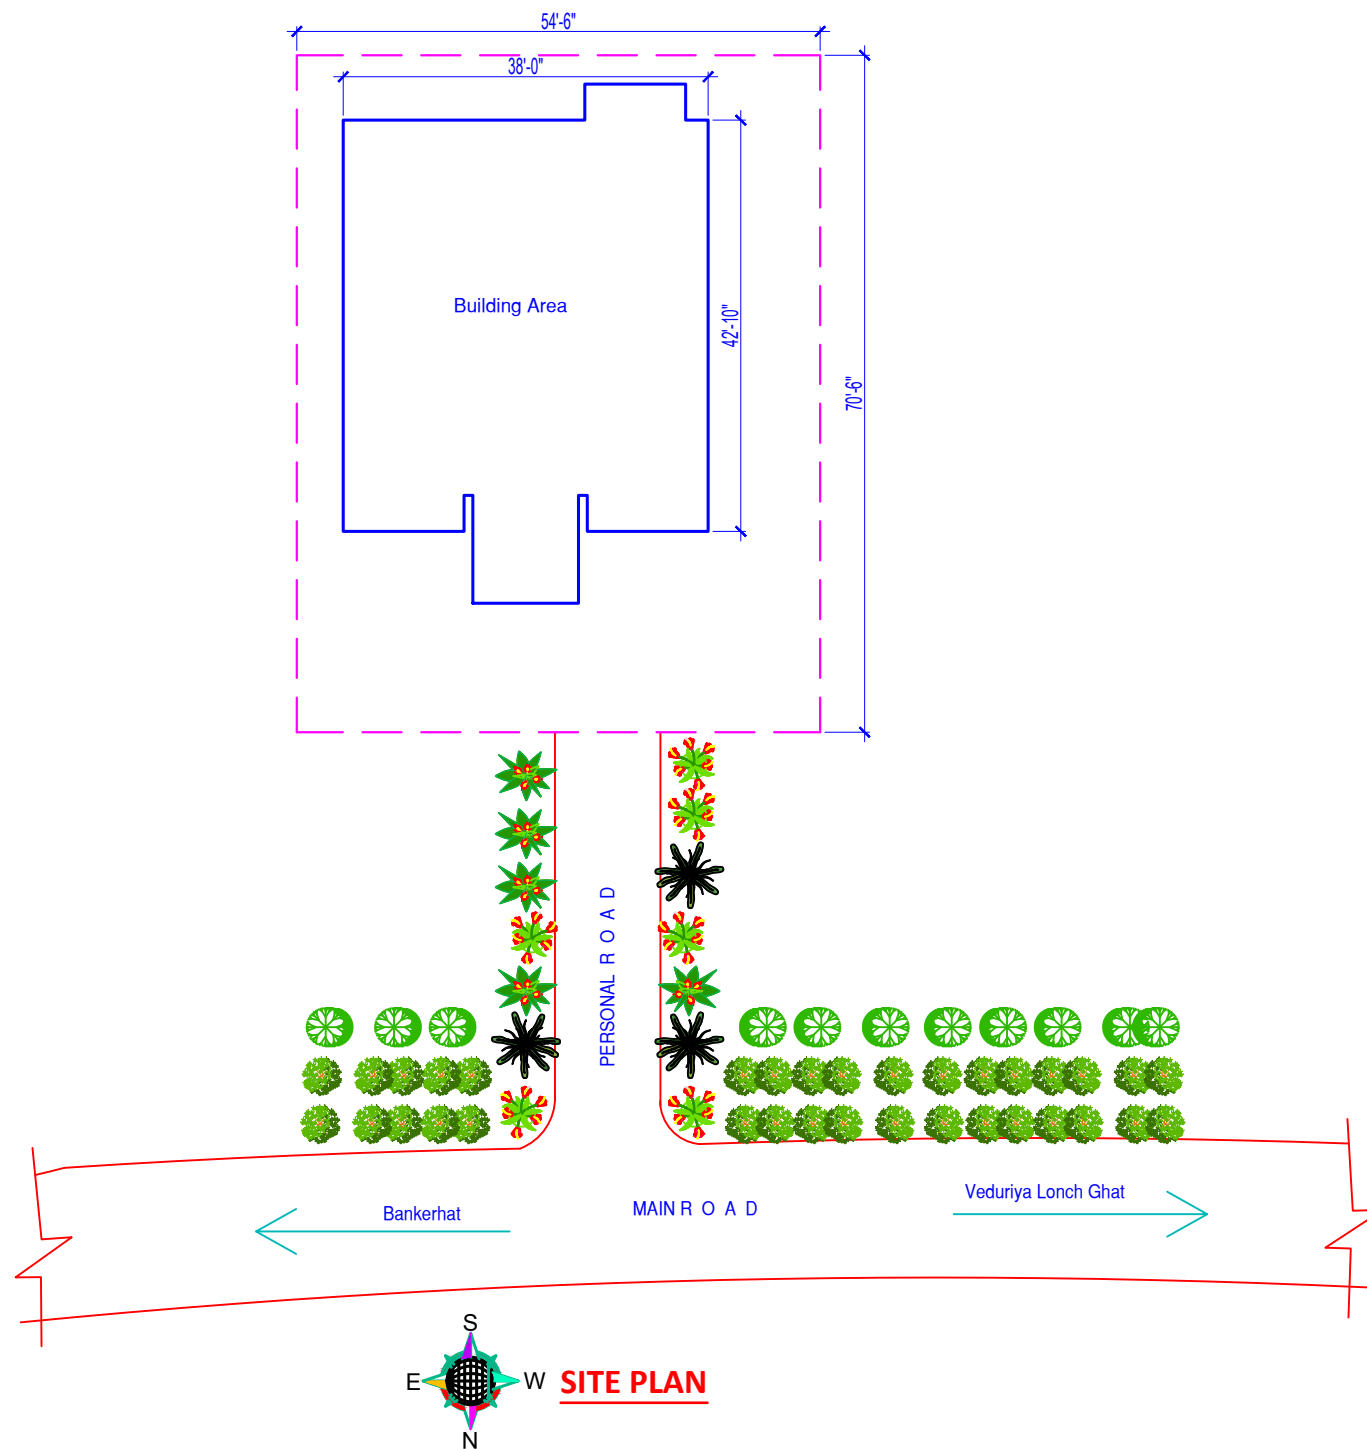


- NOTES -		
IN CASE OF ANY CONFUSION IN THE DIMENSIONS OF STRUCTURAL ELEMENT NOT TO SCALE SUCH AS - COLUMN SIZE, BEAM SIZE, SLAB THICKNESS, FALSE SLAB THICKNESS, LINTEL SIZE ETC. THE MEASUREMENT NOT TO SCALE GIVEN IN STRUCTURAL & ARCHITECTURAL DRAWINGS HAS TO BE FOLLOWED.		
- PROJECT NAME & ADDRESS -		
3- STORIED RESIDENTIAL BUILDING AT CHAR VEDURIYA, BANKERHAT , BHOLA.		
- DRAWING TITLE -		
SITE PLAN		
ARCHITECT DESIGN / DEVELOPMENT		
Architect Md. Aktaruzzaman Khokon B.Arch (DUET)		
Rahima Diploma Architect		
STRUCTURAL DESIGN / DEVELOPMENT		
Engr. Md.Hasibul Islam B.Sc in Civil (IUBAT) Senior Structure Engr.		
Md.Rashed Khan B.Sc in Civil (PU) Managing Director Building planning & Design Engineering		
SUPERVISION		
Md. Ismail Hossain Diploma in Civil Chairmen Building planning & Design Engineering		
ELECTRICAL DESIGN / DEVELOPMENT		
Md. Masum Patwary B.Sc in EEE (UIU)		
Md. Shamim Diploma in Electrical		
OWNERS NAME		
NO.	NAME	SIGNATURE
1.	MD. SHOFIQUE	
Dag No:		2332, 1888
KHATAN NO.		4007
PLOT NO.		
J.AL NO.		056
MOUZA		Char Veduria
TOTAL LAND AREA		00
 Building Planning & Design Engineering ENGINEERING SERVICE & MANAGEMENT CONSULTANTS Phone No : 01614145609 , 01884958267		
- SHEET NO. -		
A-01		
- OUTPUT -		

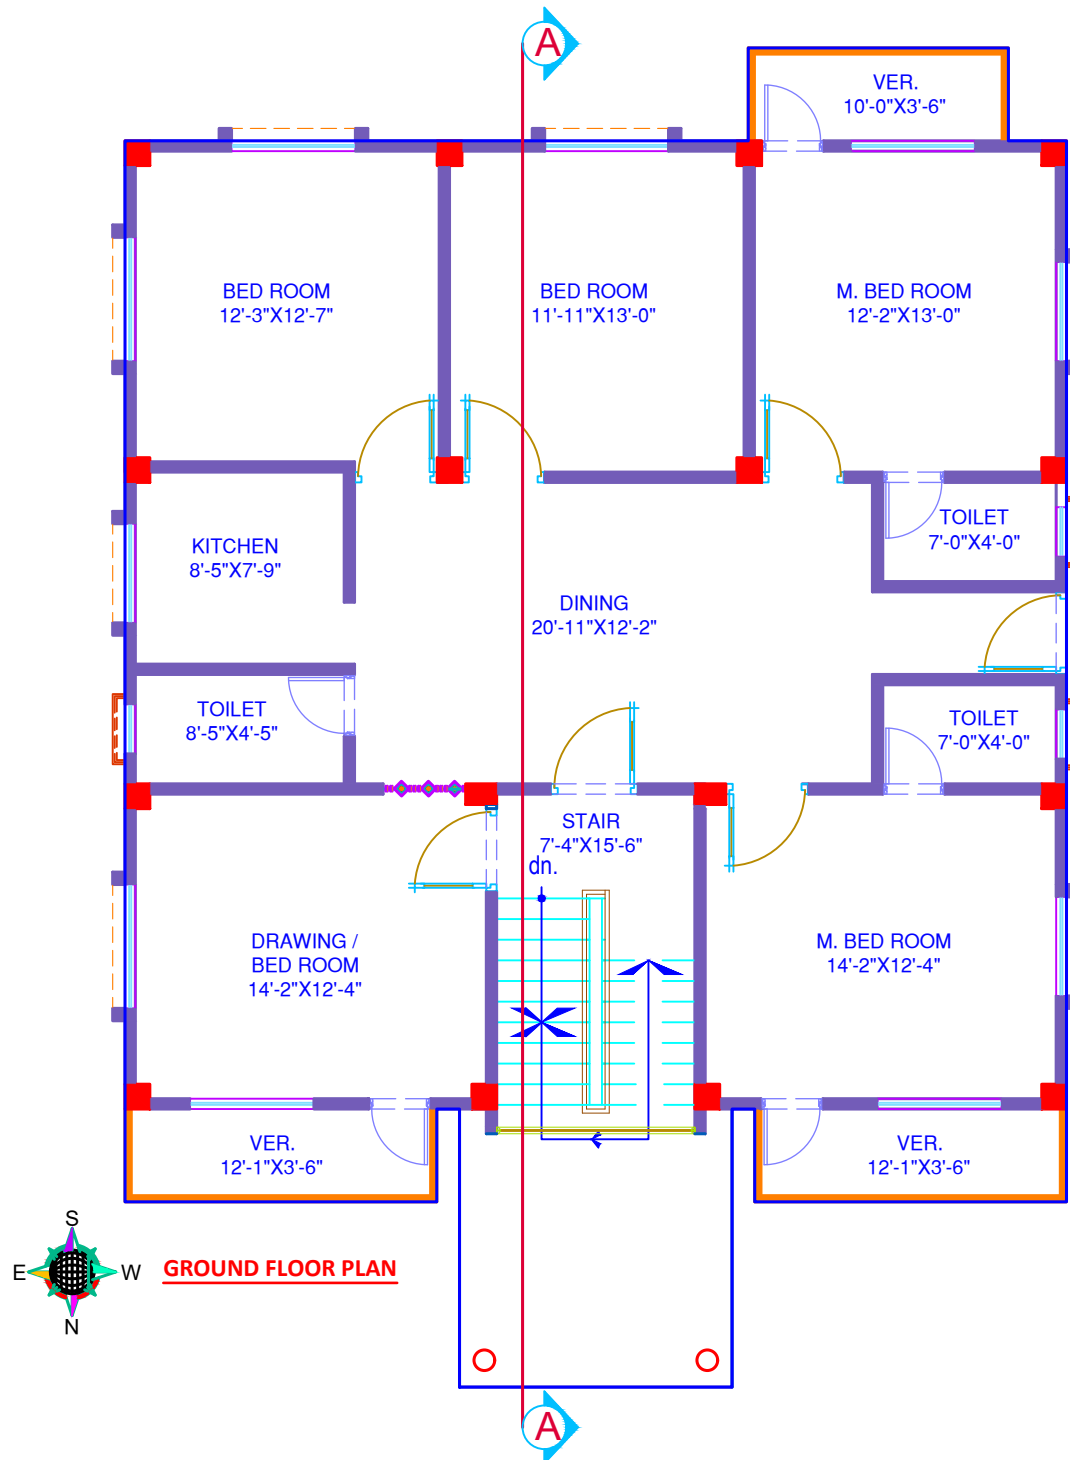


GROUND FLOOR PLAN

- NOTES -		
IN CASE OF ANY CONFUSION IN THE DIMENSIONS OF STRUCTURAL ELEMENT NOT TO SCALE SUCH AS - COLUMN SIZE, BEAM SIZE, SLAB THICKNESS, FALSE SLAB THICKNESS, LINTEL, SIZE ETC. THE MEASUREMENT NOT TO SCALE GIVEN IN STRUCTURAL & ARCHITECTURAL DRAWINGS HAS TO BE FOLLOWED.		
- PROJECT NAME & ADDRESS -		
3- STORIED RESIDENTIAL BUILDING AT CHAR VEDURIYA, BANKERHAT , BHOLA.		
- DRAWING TITLE -		
GROUND FLOOR PLAN		
ARCHITECT DESIGN / DEVELOPMENT		
Architect Md. Aktaruzzaman Khokon B.Arch (DUET)		
STRUCTURAL DESIGN / DEVELOPMENT		
Engr. Md.Hasibul Islam B.Sc in Civil (IUBAT) Senior Structure Engr.		
SUPERVISION		
Md. Rashed Khan B.Sc in Civil (PU) Managing Director Building planning & Design Engineering		
OWNERS NAME		
NO.	NAME	SIGNATURE
1.	MD. SHOFIQUE	
Dag No:		2332, 1888
KHATAN NO.		4007
PLOT NO.		
J.A.L NO.		056
MOUZA		Char Veduria
TOTAL LAND AREA		00
Building Planning & Design Engineering		
ENGINEERING SERVICE & MANAGEMENT CONSULTANTS Phone No : 01614145609 , 01884958267		
- SHEET NO. -		
A-02		
- OUTPUT -		

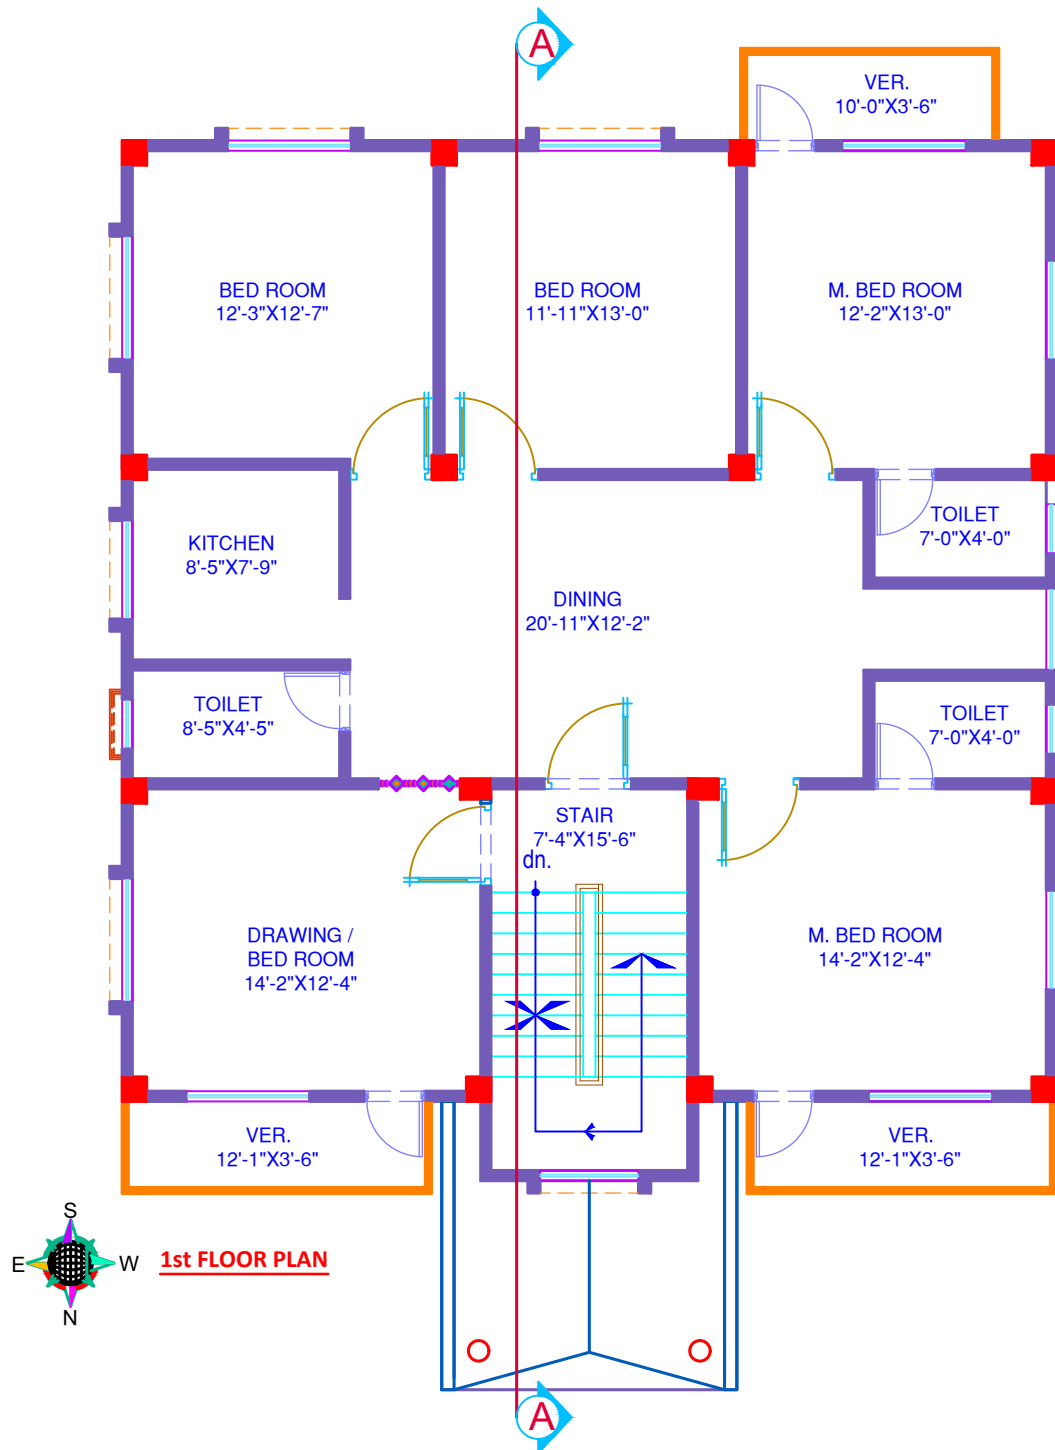


1st FLOOR PLAN

- NOTES -		
IN CASE OF ANY CONFUSION IN THE DIMENSIONS OF STRUCTURAL ELEMENT NOT TO SCALE SUCH AS - COLUMN SIZE, BEAM SIZE, SLAB THICKNESS, FALSE SLAB THICKNESS, LINTEL, SIZE ETC. THE MEASUREMENT NOT TO SCALE GIVEN IN STRUCTURAL & ARCHITECTURAL DRAWINGS HAS TO BE FOLLOWED.		
- PROJECT NAME & ADDRESS -		
3- STORIED RESIDENTIAL BUILDING AT CHAR VEDURIYA, BANKERHAT , BHOLA.		
- DRAWING TITLE -		
1ST FLOOR PLAN		
ARCHITECT DESIGN / DEVELOPMENT		
Architect Md. Aktaruzzaman Khokon B.Arch (DUET)		
Rahima Diploma Architect		
STRUCTURAL DESIGN / DEVELOPMENT		
Engr. Md.Hasibul Islam B.Sc in Civil (IUBAT) Senior Structure Engr.		
Md.Rashed Khan B.Sc in Civil (PU) Managing Director Building planning & Design Engineering		
SUPERVISION		
Md. Ismail Hossain Diploma in Civil Chairmen Building planning & Design Engineering		
ELECTRICAL DESIGN / DEVELOPMENT		
Md. Masum Patwary B.Sc in EEE (JILU)		
Md. Shamim Diploma in Electrical		
OWNERS NAME		
NO.	NAME	SIGNATURE
1.	MD. SHOFIQUE	
Dag No:		2332, 1888
KHATAN NO.		4007
PLOT NO.		
J.AL NO.		056
MOUZA		Char Veduria
TOTAL LAND AREA		00
 Building Planning & Design Engineering ENGINEERING SERVICE & MANAGEMENT CONSULTANTS Phone No : 01614145609 , 01884958267		
- SHEET NO. -		
A-03		
- OUTPUT -		

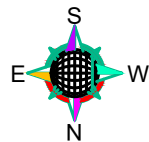

2nd FLOOR PLAN

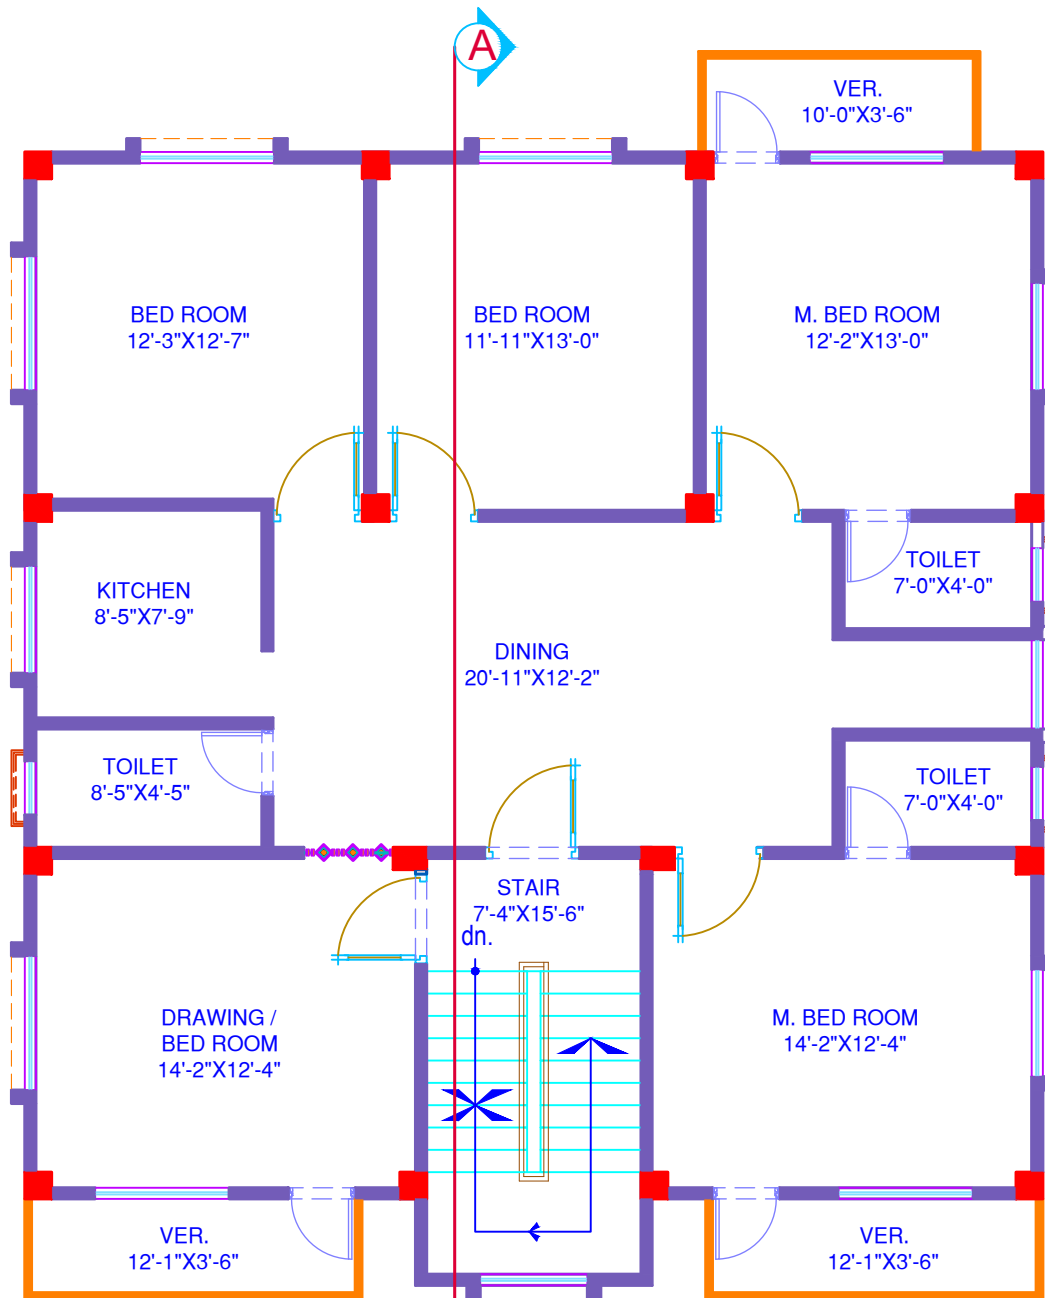

- NOTES -

IN CASE OF ANY CONFUSION IN THE DIMENSIONS OF STRUCTURAL ELEMENT NOT TO SCALE SUCH AS - COLUMN SIZE, BEAM SIZE, SLAB THICKNESS, FALSE SLAB THICKNESS, LINTEL SIZE ETC. THE MEASUREMENT NOT TO SCALE GIVEN IN STRUCTURAL & ARCHITECTURAL DRAWINGS HAS TO BE FOLLOWED.

- PROJECT NAME & ADDRESS -

3- STORIED RESIDENTIAL BUILDING AT CHAR VEDURIYA, BANKERHAT , BHOLA.

- DRAWING TITLE -

2ND FLOOR PLAN

ARCHITECT DESIGN / DEVELOPMENT

Architect Md. Aktaruzzaman Khokon
B.Arch (DUET)

Rahima

Diploma Architect

STRUCTURAL DESIGN / DEVELOPMENT

Engr. Md.Hasibul Islam

B.Sc in Civil (IUBAT)
Senior Structure Engr.

Md.Rashed Khan

B.Sc in Civil (PU)
Managing Director
Building planning & Design Engineering

SUPERVISION

Md. Ismail Hossain

Diploma in Civil
Chairmen
Building planning & Design Engineering

ELECTRICAL DESIGN / DEVELOPMENT

Md. Masum Patwary

B.Sc in EEE (IUB)

Md. Shamim

Diploma in Electrical

OWNERS NAME

NO.	NAME	SIGNATURE
1.	MD. SHOFIQUE	

Dag No:	2332, 1888
KHATAN NO.	4007
PLOT NO.	
J.AL NO.	056
MOUZA	Char Veduria
TOTAL LAND AREA	00





**Building Planning &
Design Engineering**

ENGINEERING SERVICE & MANAGEMENT CONSULTANTS
Phone No : 01614145609 , 01884958267

- SHEET NO. -


A-04

- OUTPUT -

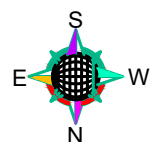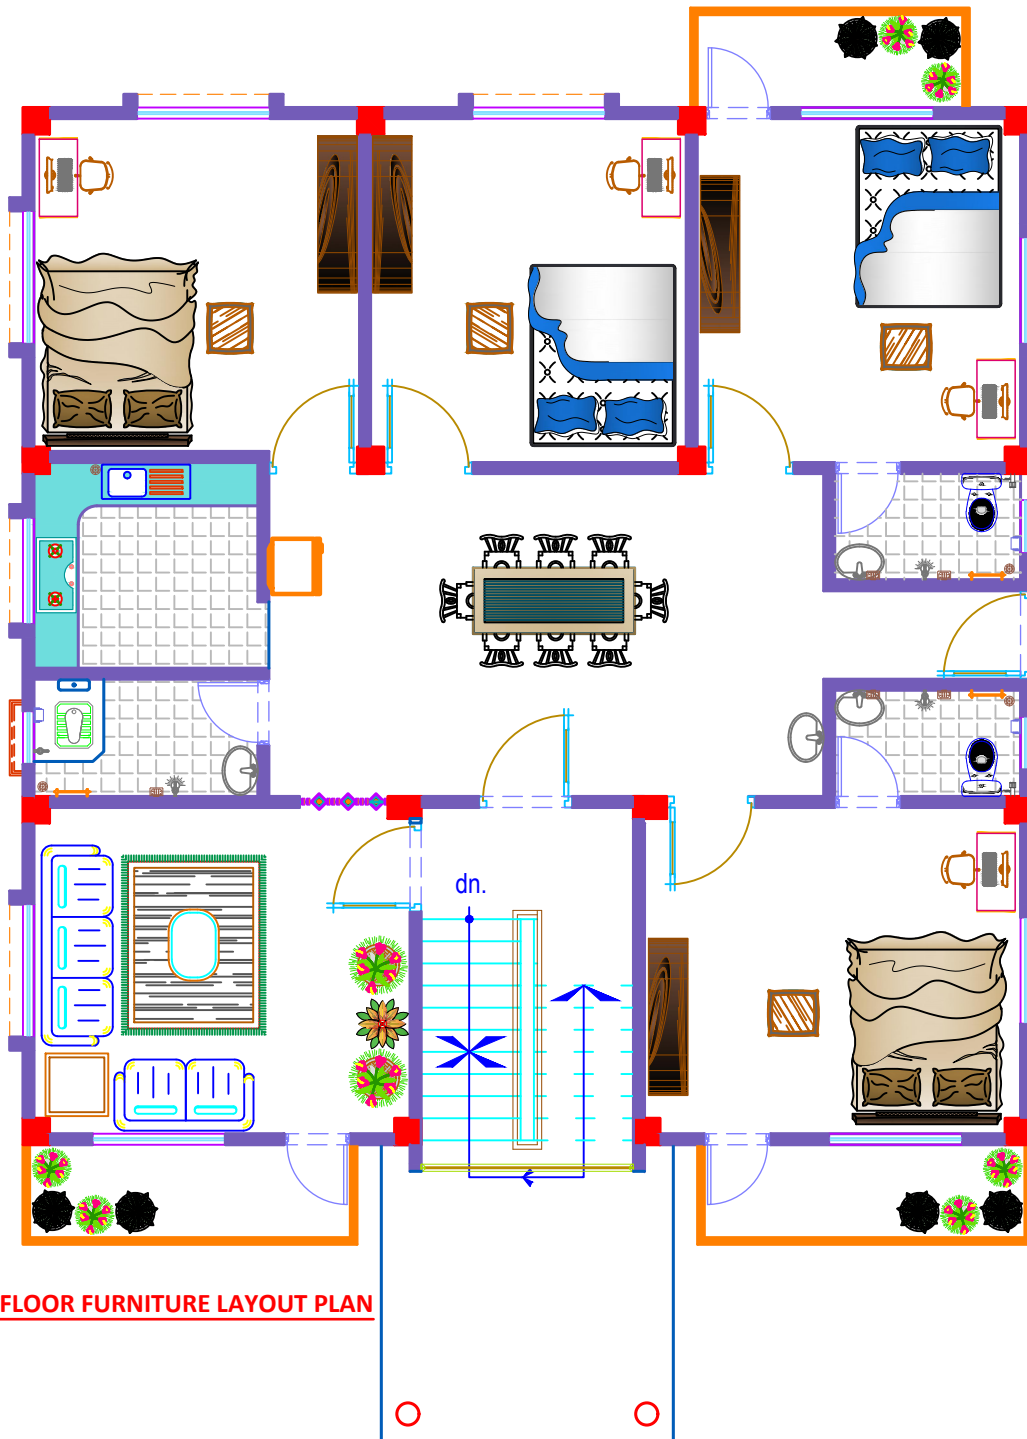


GROUND FLOOR FURNITURE LAYOUT PLAN

- NOTES -		
IN CASE OF ANY CONFUSION IN THE DIMENSIONS OF STRUCTURAL ELEMENT NOT TO SCALE SUCH AS - COLUMN SIZE, BEAM SIZE, SLAB THICKNESS, FALSE SLAB THICKNESS, LINTEL, SIZE ETC. THE MEASUREMENT NOT TO SCALE GIVEN IN STRUCTURAL & ARCHITECTURAL DRAWINGS HAS TO BE FOLLOWED.		
- PROJECT NAME & ADDRESS -		
3- STORIED RESIDENTIAL BUILDING AT CHAR VEDURIYA, BANKERHAT , BHOLA.		
- DRAWING TITLE -		
GROUND FLOOR FURNITURE LAY-OUT PLAN		
ARCHITECT DESIGN / DEVELOPMENT		
Architect Md. Aktaruzzaman Khokon B.Arch (DUET)		
Rahima Diploma Architect		
STRUCTURAL DESIGN / DEVELOPMENT		
Engr. Md.Hasibul Islam B.Sc in Civil (IUBAT) Senior Structure Engr.		
Md.Rashed Khan B.Sc in Civil (PU) Managing Director Building planning & Design Engineering		
SUPERVISION		
Md. Ismail Hossain Diploma in Civil Chairmen Building planning & Design Engineering		
ELECTRICAL DESIGN / DEVELOPMENT		
Md. Masum Patwary B.Sc in EEE (JILU)		
Md. Shamim Diploma in Electrical		
OWNERS NAME		
NO.	NAME	SIGNATURE
1.	MD. SHOFIQUE	
Dag No.	2332, 1888	
KHATAN NO.	4007	
PLOT NO.		
JAL NO.	056	
MOUZA	Char Veduria	
TOTAL LAND AREA	00	
		
Building Planning & Design Engineering		
ENGINEERING SERVICE & MANAGEMENT CONSULTANTS		
Phone No : 01614145609 , 01884958267		
- SHEET NO. -		
A-05		
- OUTPUT -		

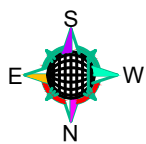

1ST FLOOR FURNITURE LAYOUT PLAN

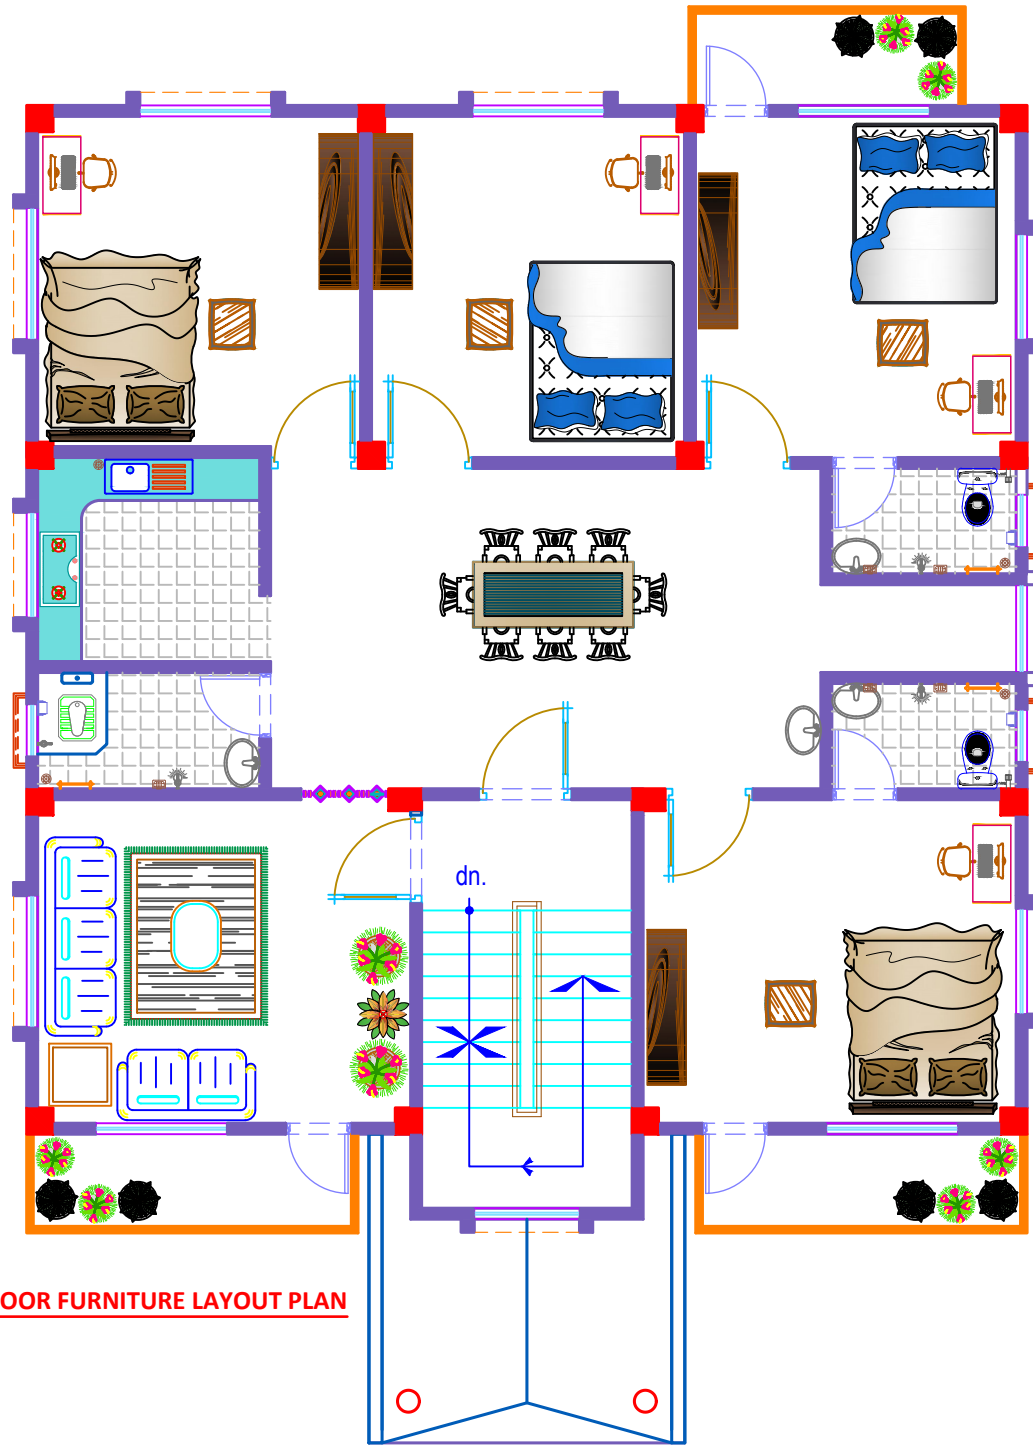

- NOTES -

IN CASE OF ANY CONFUSION IN THE DIMENSIONS OF STRUCTURAL ELEMENT NOT TO SCALE SUCH AS - COLUMN SIZE, BEAM SIZE, SLAB THICKNESS, FALSE SLAB THICKNESS, LINTEL, SIZE ETC. THE MEASUREMENT NOT TO SCALE GIVEN IN STRUCTURAL & ARCHITECTURAL DRAWINGS HAS TO BE FOLLOWED.

- PROJECT NAME & ADDRESS -

3- STORIED RESIDENTIAL BUILDING AT CHAR VEDURIYA, BANKERHAT , BHOLA.

- DRAWING TITLE -

1ST FLOOR FURNITURE LAYOUT PLAN

ARCHITECT DESIGN / DEVELOPMENT

Architect Md. Aktaruzzaman Khokon
B.Arch (DUET)

Rahima
Diploma Architect

STRUCTURAL DESIGN / DEVELOPMENT

Engr. Md.Hasibul Islam
B.Sc in Civil (IUBAT)
Senior Structure Engr.

Md.Rashed Khan
B.Sc in Civil (PU)
Managing Director
Building planning & Design Engineering

SUPERVISION

Md. Ismail Hossain
Diploma in Civil
Chairmen
Building planning & Design Engineering

ELECTRICAL DESIGN / DEVELOPMENT

Md. Masum Patwary
B.Sc in EEE (JILU)

Md. Shamim
Diploma in Electrical

OWNERS NAME

NO.	NAME	SIGNATURE
1.	MD. SHOFIQUE	


Dag No.	2332, 1888
KHATAN NO.	4007
PLOT NO.	
J.AL NO.	056
MOUZA	Char Veduria
TOTAL LAND AREA	00

Building Planning & Design Engineering
ENGINEERING SERVICE & MANAGEMENT CONSULTANTS
Phone No : 01614145609 , 01884958267

- SHEET NO. -

A-06

- OUTPUT -

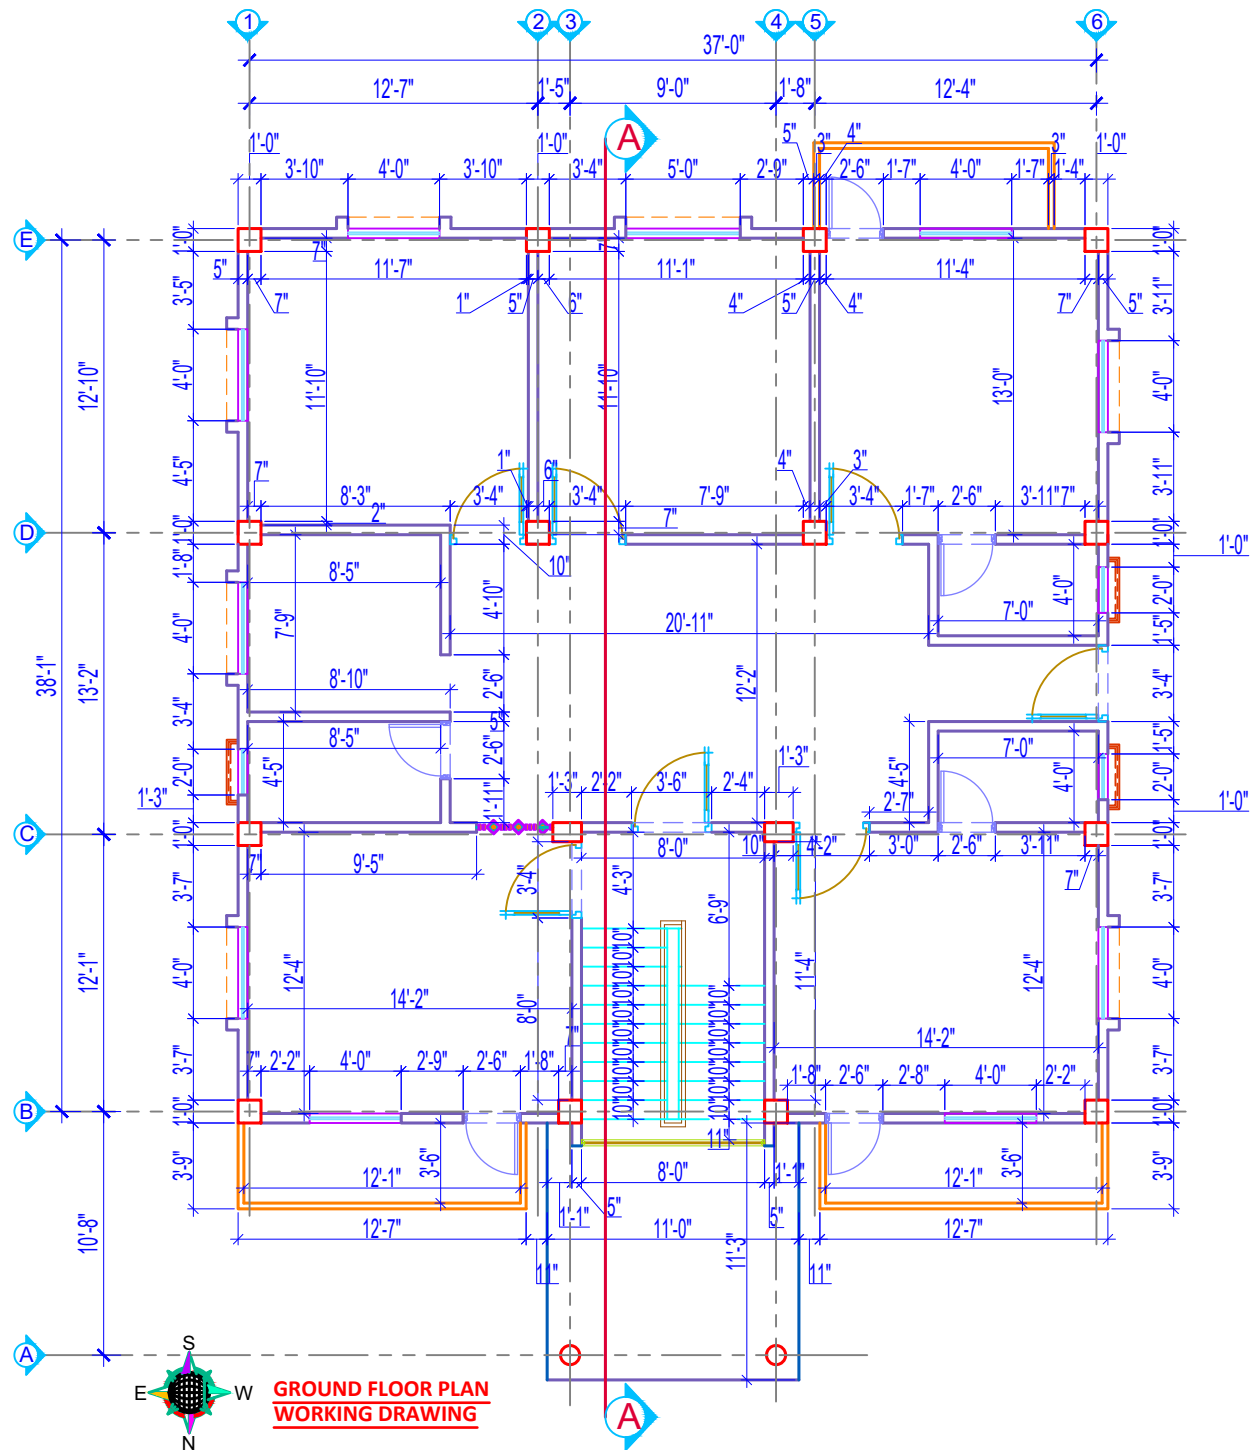

- NOTES -

IN CASE OF ANY CONFUSION IN THE DIMENSIONS OF STRUCTURAL ELEMENT NOT TO SCALE SUCH AS - COLUMN SIZE, BEAM SIZE, SLAB THICKNESS, FALSE SLAB THICKNESS, LINTEL, SIZE ETC. THE MEASUREMENT NOT TO SCALE GIVEN IN STRUCTURAL & ARCHITECTURAL DRAWINGS HAS TO BE FOLLOWED.

- PROJECT NAME & ADDRESS -

3- STORIED RESIDENTIAL BUILDING AT CHAR VEDURIYA, BANKERHAT, BHOLA.

- DRAWING TITLE -

GROUND FLOOR WORKING DRAWING

ARCHITECT DESIGN / DEVELOPMENT

Architect Md. Aktaruzzaman Khokon
B.Arch (DUET)

Rahima
Diploma Architect

STRUCTURAL DESIGN / DEVELOPMENT

Engr. Md.Hasibul Islam
B.Sc in Civil (IUBAT)
Senior Structure Engr.

Md.Rashed Khan
B.Sc in Civil (PU)
Managing Director
Building planning & Design Engineering

SUPERVISION

Md. Ismail Hossain
Diploma in Civil
Chairman
Building planning & Design Engineering

ELECTRICAL DESIGN / DEVELOPMENT

Md. Masum Patwary
B.Sc in EEE (JUI)

Md. Shamim
Diploma in Electrical

OWNERS NAME		
NO.	NAME	SIGNATURE
1.	MD. SHOFIQUE	

Dag No:	2332, 1888
KHATAN NO.	4007
PLOT NO.	
JAL NO.	056
MOUZA	Char Veduria
TOTAL LAND AREA	00




Building Planning & Design Engineering
ENGINEERING SERVICE & MANAGEMENT CONSULTANTS
Phone No : 01614145609 , 01884958267

- SHEET NO. -
A-07
- OUTPUT -

PROJECT :

**PROPOSED 3(THREE) STORIED RESIDENTIAL BUILDING
FOR MD.SHOFIQUE AT AT CHAR VEDURIA,BANKERHAT,BHOLA,BANGLADESH.
KHATIAN NO:-4007,JL NO:-056,DAG NO:-2332,1888**

DATE: 25-01-2026

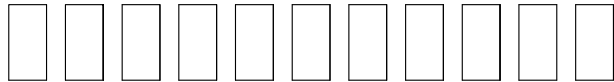

STRUCTURAL DRAWING

GENERAL NOTES

2. FOUNDATION

- THE BUILDING HAS BEEN DESIGN FOR 3-STORIED RESIDENTIAL BUILDING AT VEDURIA, BANKERHAT, BHOLA, BANGLADESH.
- FOUNDATION TYPE- FOOTING FOUNDATION
- DEPTH OF FOUNDATION AS PER STRUCTURAL DRAWING.

3. CONCRETE :

- TYPE : CONCRETE COMPRESSIVE STRENGTH CONSIDERED AS FOLLOWS
1) COLUMN CONCRETE $f_c = 3000\text{psi}$.

- SLAB, PILE CAP AND OTHERS CONCRETE f_c 3000psi

WHICH ARE TO BE CONFORMED BY TRAIL MIX DESIGN
RATIO 1:1.5:3 WITH STONE CHIPS

- MINIMUM CYLINDER STRENGTH : BASED ON CYLINDER TEST OF

DIAMETER $D = 4"(100\text{mm})$ & HEIGHT = $8"(200\text{mm})$

- 7 DAYS STRENGTH For 3000psi need min2170psi
For 3500psi need min2500psi

- 28 DAYS STRENGTH For 3000psi need 3100psi
For 3500psi need 3850psi

- CURING OF R.C.C WORK :

- CURING TIME MINIMUM 28 DAYS

- METHOD OF CURING :

- * HORIZONTAL SURFACE - BY PONDING OF WATER
- * OTHER SURFACES-BY WRAPPING MOIST JUTE FABRIC AND SPRINKLING WATER BY HOSE PIPE FREQUENTLY.

4. CEMENT

ORDINARY PORTLAND CEMENT CONFORMING TO BDS 232:1974/ASTM C150

5. CONCRETE AGGREGATE

- FINE AGGREGATES : SAND OF F.M 2.0 (Min.)
- COARSE AGGREGATES: 20mm DOWN WELL GRADED STONE CHIPS TO BE USED AS COARSE AGGREGATE IN ALL R.C.C. WORK EXCEPT RAILING, DROPWALL FINS FOR WHICH 12mm DOWN GRADED STONE CHIPS TO BE USED.

6. WATER

POTABLE WATER TO BE USED IN CONCRETE MIX

7. STEEL REINFORCEMENT

- ALL FOOTING, COLUMN & BEAM REINFORCEMENTS ARE 60 GRADE HIGH STRENGTH DEFORMED BAR MADE FROM BILLET STEEL
- YIELD STRENGTH OFF STEEL $f_y = 415$ Mpa (60000 psi) DEFORMED TO ONE OF THE FOLLOWING SPECIFICATIONS :1) BDS 1313 : 1991, 1) ASTM A615M
- THE FOLLOWING TESTS FOR REINFORCING BARS FROM RANDOM SAMPLES SHALL BE CONDUCTED AT BUET AS PER BDS 1313 : 1991
- CONDUCTED AT BUET AS PER BDS 1313:1991
 - TENSILE STRENGTH TEST
 - PERCENTAGE ELONGATION TEST
 - BEND/REBEND TEST

8. LAP LENGTH

UNLESS OTHERWISE MENTIONED IN THE DRAWINGS, LAP LENGTH OF BARS SHALL BE : $f_c=24\text{MPa}, f_y=60\text{ksi}$

BAR DIA (mm)	TENSION (INCH)	COMPRESSION (INCH)
10#	38	12
12#	38	15
16#	38	18
20#	38	24
22#	62	25
25#	62	30

COLUMN LAPS SHALL BE TENSION LAPS

9. HOOKS OF REBAR

- FOR ALL RE-BAR : PROVIDE 90° STANDARD HOOKS (L-BENT) IF NOT SHOWN IN THE DRAWINGS.

10. SPACER BARS


TO SUPPORT SECOND LAYER BARS IN BEAMS/SLABS, USE 25# SPACER BARS @ 1200 M/M C/C WHERE REQUIRED.

11. CHAIRS

USE CHAIRS OF NECESSARY DIMENSION MADE OF 10# /12#/16# BAR TO SUPPORT TOP BARS OF SLAB @ 1200 MM C/C

12. LAP LOCATION :

- FOR BEAM BOTTOM BAR, LAP NOT TO BE PROVIDED AT MIDDLE THIRD ZONE OF THE SPAN
- FOR BEAM TOP BAR, LAP MAY BE PROVIDED AT MIDDLE THIRD ZONE OF THE SPAN
- NOT MORE THAN 50% OF THE BARS SHALL BE SPLICED AT ONE PLACE
- LAP SPLICES ARE TO BE CONFINED BY HOOPS WITH MAXIMUM SPACING OR PITCH OF $d/4$ OR 4 " WHERE d IS THE EFFECTIVE DEPTH OF THE BEAM.

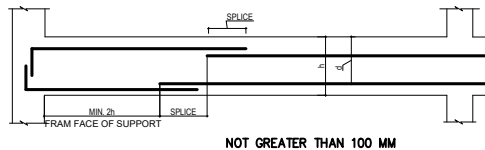

13. DEVELOPMENT LENGTH

ALL BEAM AND SLAB REBARS SHOULD BE EXTENDED INTO THE SUPPORT UPTO DEVELOPMENT LENGTH.

14. ADMIXTURE

APORVAL BY THE ENGINEER

15. WATER STOPPER

225 MM WIDE PVC WATER STOPPER TO BE USED AT ALL CONSTRUCTION JOINTS BELOW GROUND IN MAT, SHEAR WALL, WATER TANK WALL ETC.

16. CORNER REINFORCEMENT ('CR')

CORNER REINFORCEMENT FOR BEAM SUPPORTED 2 -WAY SLABS

17. CONCRETE CLEAR COVER FOR REINFORCING BARS

Member	Location or Condition	Thickness of Cover	Figure
mat and pile cap	side	3"	
	bottom	3"	
column	above P.L	1.5"	
	Below P.L	2.5"	
Wall	below P.L	2.5"	
beam	top, side	** 1.5"	
	bottom	** 1.5"	
slab and stair	top and bottom	.75"	
	exterior	2.5"	
Retain wall	interior	1.5"	
	water face	2"	
water tank	other face	2.5"	

- * from tie
- ** from stirrups

18. MAXIMUM BARS IN BEAMS IN SINGLE LAYER

MAXIMUM NUMBER OF BARS AS A SINGLE LAYER IN BEAM STEM SHALL BE AS PER ACI DETAILING MANUAL 1994.


19. MINIMUM BAR SPACING OF COLUMN

LONGITUDINAL BARS

CLEAR DISTANCE BETWEEN LONGITUDINAL BARS SHALL NOT BE LESS THAN 1.5 TIMES BAR DIAMETER, 1.5 TIMES THE SIZE OF COURSE AGGREGATE NOR 40mm.

SCHEDULE OF LINTEL

Width of Lintel	Clear Span	Size & Rebar
5"	Up to 6'-0"	5" 4-12mm# 8mm.# @ 5"c/c
5"	6'-1" to 9'-0"	5" 4-12mm# 8mm.# @ 5"c/c
10"	Up to 6'-0"	10" 4-12mm# 8mm.# @ 6"c/c
10"	6'-1" to 9'-0"	10" 5-12mm# 8mm.# @ 6"c/c
5"	9'-1" to 12'-0"	5" 4-12mm# 8mm.# @ 5"c/c

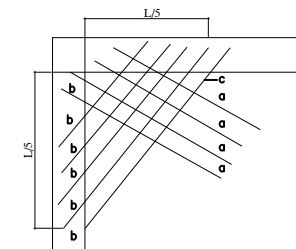

L= LONGER CLEAR SPAN.

a= TOP BARS

b= BOTTOM BARS

a=c.

SPACING OF CORNER BARS= SPACING OF MAXIMUM POSITIVE BARS

- NOTES -

IN CASE OF ANY CONFUSION IN THE DIMENSIONS OF STRUCTURAL ELEMENT NOT TO SCALE SUCH AS - COLUMN SIZE, BEAM SIZE, SLAB THICKNESS, FALSE SLAB THICKNESS, LINTEL SIZE ETC. THE MEASUREMENT NOT TO SCALE GIVEN IN STRUCTURAL & ARCHITECTURAL DRAWINGS HAS TO BE FOLLOWED.

- PROJECT NAME & ADDRESS -

3- STORIED RESIDENTIAL BUILDING AT CHAR VEDURIYA, BANKERHAT, BHOLA.

- DRAWING TITLE -

GENERAL NOTES

ARCHITECT DESIGN / DEVELOPMENT

Architect Md. Aktaruzzaman Khokon

B.Arch (DUET)

Rahima

Diploma Architect

STRUCTURAL DESIGN / DEVELOPMENT

Engr. Md.Hasibul Islam

B.Sc in Civil (IUBAT)

Senior Structure Engr.

Md.Rashed Khan

B.Sc in Civil (PU)

Managing Director

Building planning & Design Engineering

SUPERVISION

Md. Ismail Hossain

Diploma in Civil

Chairman

Building planning & Design Engineering

ELECTRICAL DESIGN / DEVELOPMENT

Md. Masum Patwary

B.Sc in EEE (UIU)

Md. Shamim

Diploma in Electrical

OWNERS NAME

NO.	NAME	SIGNATURE
1.	MD. SHOFIQUE	

Dag No:	2332, 1888
KHATIAN NO.	4007
PLOT NO.	
J.A.L NO.	056
MOUZA	Char Veduria
TOTAL LAND AREA	3842 Sit



Building Planning & Design Engineering

ENGINEERING SERVICE & MANAGEMENT CONSULTANTS
Phone No : 01614145609 , 01884958267


- SHEET NO. -

G-01


- OUTPUT -

20. SLAB END REINFORCING DETAILS

- a) FREE END OF SLAB INCAPABLE OF EMBEDDING OF STEEL BAR IN BEAM/WALL
b) OTHERS

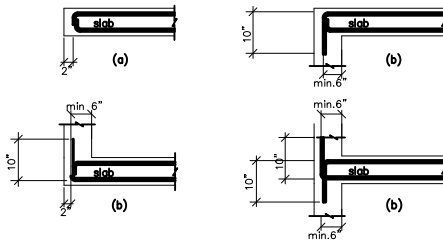

21. REINFORCEMENT DETAILS FOR SLAB OPENINGS

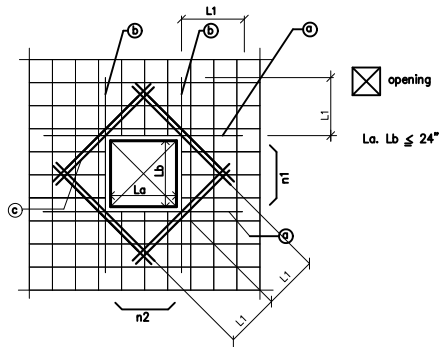


n1, n2 : The number of bars which are cut off for opening

- ① The number of extra bars > n1/2 (top and bott bars)
② The number of extra bars > n2/2 (top and bott bars)
③ The number of extra bars = 2-D12 (top and bott bars)

22. RECOMMENDED END HOOKS

bar hook	Form and Extention	Bend Angle (degree)	Bend Radius (r)	Used Bar	Location
primary reinf.		180°	r = 2db	6 to 25	lap splice end of anchorage
tie/stirrups		135°	r = 1.25db	6 to 12	stirrups fastening bar diagonal hoop
primary reinf.		90°	r = 2.5db	6 to 32	bend-up for embedment
slab		45°	r = 5db	8 to 20	bend bar in slab


23. SCOPE OF EMBEDMENT

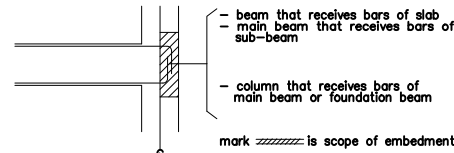

24. OPENING IN R.C.C WALLS


NOT LESS THAN THREE NO. 20Ø BARS SHALL BE PROVIDED AROUND ALL DOOR AND WINDOW OPENINGS IN R.C.C WALLS. THE BAR SHALL BE EXTENDED BEYOND THE CORNERS OF THE OPENINGS TO A DISTANCE EQUAL TO THE DEVELOPMENT LENGTH BUT NOT LESS THAN 600 MM.

25. END HOOK OF STIRRUPS

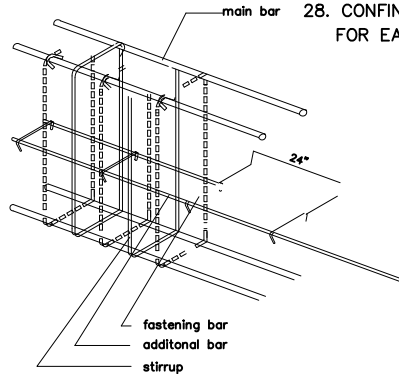

END HOOKS OF STIRRUPS ARE LOCATED ALTERNATELY AT TOP CORNER BAR OF THE SECTION.


26. COLUMN SPLICE LOCATION

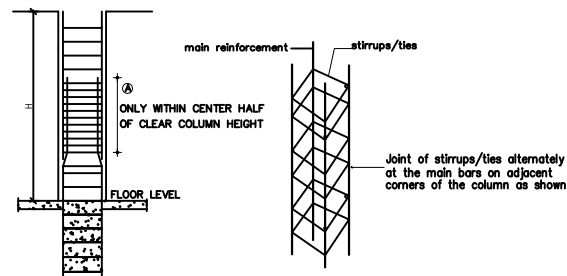

Ⓐ IS AREA FOR SPLICE OF COLUMN REINFORCEMENT. MAXIMUM 50% OF TOTAL BAR IS SPLICED AT ONE LEVEL.

H = CLEAR COLUMN HEIGHT


27. CONFINEMENT REQUIREMENTS OF COLUMN AT JOINTS FOR EARTHQUAKE LOADING

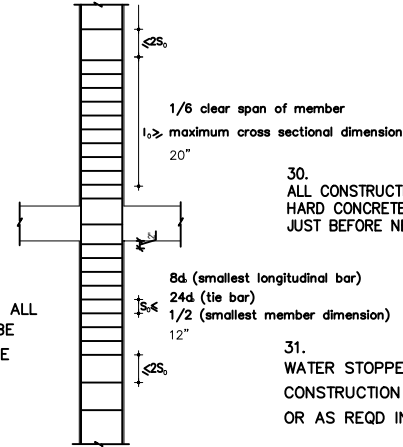

30. ALL CONSTRUCTION JOINT MUST BE CHIPPED TO EXPOSE HARD CONCRETE, WETTED AND GROUTED WITH GREEN MORTAR JUST BEFORE NEW CONCRETE IS POURED.

31. WATER STOPPER SHALL BE USED FOR ALL VERTICAL CONSTRUCTION JOINT WITH PVC STOPPER (MIN 9" LONG). OR AS REQD IN CONSULTATION WITH THE CONSULTANT.

28. CONFINEMENT REQUIREMENTS OF BEAM AT JOINTS FOR EARTHQUAKE LOADING

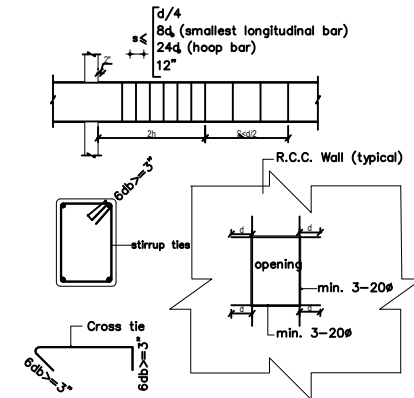

29. BAR CURTAILMENT (FLAT SLAB)

TOP BARS.	100%
	C₁ of support L1/3 C₂ of support L2/3 C₃ of support L2/3 EXT. SUPPORT INT. SUPPORT INT. SUPPORT L2+L1
BOTTOM BARS.	100%
	C₁ C₂ C₃

NOTES

IN CASE OF ANY CONFUSION IN THE DIMENSIONS OF STRUCTURAL ELEMENT NOT TO SCALE SUCH AS - COLUMN SIZE, BEAM SIZE, SLAB THICKNESS, FALSE SLAB THICKNESS, LINTEL SIZE ETC. THE MEASUREMENT NOT TO SCALE GIVEN IN STRUCTURAL & ARCHITECTURAL DRAWINGS HAS TO BE FOLLOWED.

- PROJECT NAME & ADDRESS -

3- STORIED RESIDENTIAL BUILDING AT CHAR VEDURIYA, BANKERHAT, BHOLA.

- DRAWING TITLE -

GENERAL NOTES

ARCHITECT DESIGN / DEVELOPMENT

Architect Md. Aktaruzzaman Khokon
B.Arch (DUET)

Rahima

Diploma Architect

STRUCTURAL DESIGN / DEVELOPMENT

Engr. Md.Hasibul Islam
B.Sc in Civil (IUBAT)
Senior Structure Engr.

Md.Rashed Khan

B.Sc in Civil (PU)
Managing Director
Building planning & Design Engineering

SUPERVISION

Md. Ismail Hossain
Diploma in Civil
Chairman

Building planning & Design Engineering

ELECTRICAL DESIGN / DEVELOPMENT

Md. Masum Patwary
B.Sc in EEE (UIU)

Md. Shamim

Diploma in Electrical

OWNERS NAME

NO.	NAME	SIGNATURE
1.	MD. SHOFIQUE	

Dag No:	2332, 1888
KHATIAN NO.	4007
PLOT NO.	
J.A.L. NO.	056
MOUZA	Char Veduria
TOTAL LAND AREA	3842 Sft




Building Planning & Design Engineering

ENGINEERING SERVICE & MANAGEMENT CONSULTANTS
Phone No : 01614145609 , 01884958267

- SHEET NO. -

G-02

- OUTPUT -

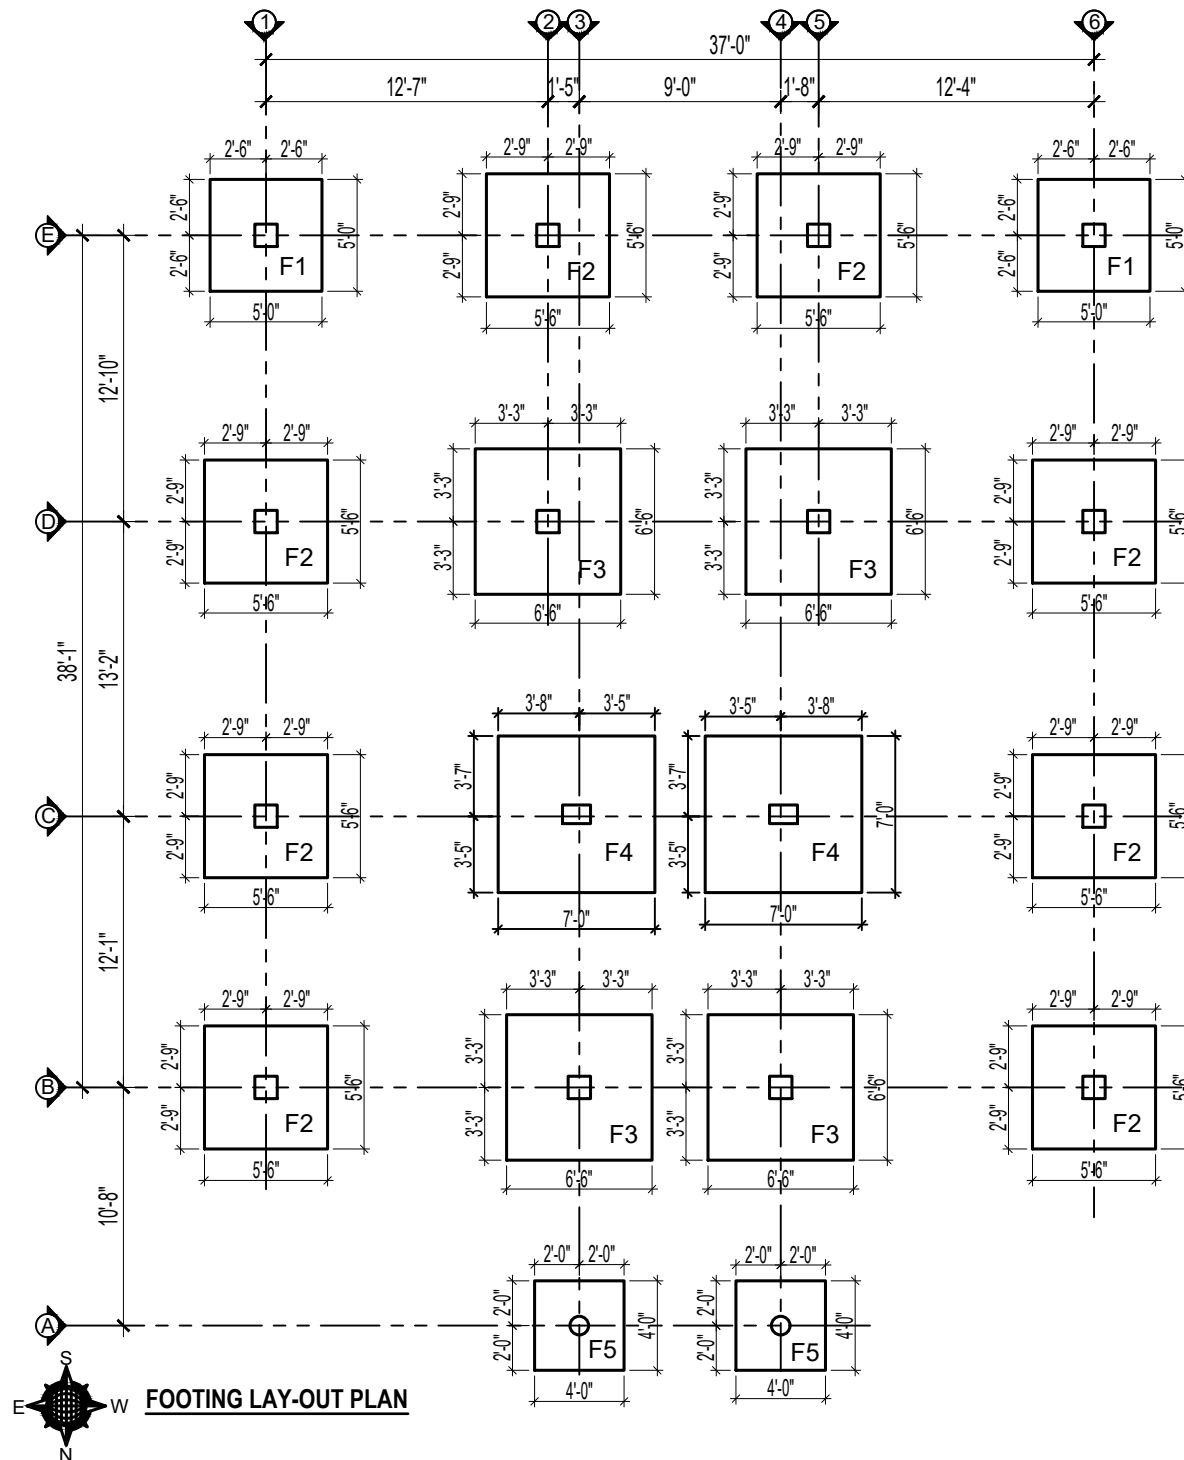

FOOTING LAY-OUT PLAN

NOTES -

IN CASE OF ANY CONFUSION IN THE DIMENSIONS OF STRUCTURAL ELEMENT NOT TO SCALE SUCH AS - COLUMN SIZE, BEAM SIZE, SLAB THICKNESS, FALSE SLAB THICKNESS, LINTEL SIZE ETC. THE MEASUREMENT NOT TO SCALE GIVEN IN STRUCTURAL & ARCHITECTURAL DRAWINGS HAS TO BE FOLLOWED.

PROJECT NAME & ADDRESS -

3- STORIED RESIDENTIAL BUILDING AT CHAR VEDURIYA, BANKERHAT , BHOLA.

DRAWING TITLE -

FOOTING LAY-OUT PLAN

ARCHITECT DESIGN / DEVELOPMENT

Architect Md. Aktaruzzaman Khokon
B.Arch (DUET)

Rahima
Diploma Architect

STRUCTURAL DESIGN / DEVELOPMENT

Engr. Md.Hasibul Islam
B.Sc in Civil (IUBAT)
Senior Structure Engr.

Md.Rashed Khan
B.Sc in Civil (PU)
Managing Director
Building planning & Design Engineering

SUPERVISION

Md. Ismail Hossain
Diploma in Civil
Chairman
Building planning & Design Engineering

ELECTRICAL DESIGN / DEVELOPMENT

Md. Masum Patwary
B.Sc in EEE (UIU)

Md. Shamim
Diploma in Electrical

OWNERS NAME

NO.	NAME	SIGNATURE
1.	MD. SHOFIQUE	

Dag No:	2332, 1888
KHATAN NO.	4007
PLOT NO.	
J.AL NO.	056
MOUZA	Char Veduria
TOTAL LAND AREA	3842 Sft




Building Planning & Design Engineering
ENGINEERING SERVICE & MANAGEMENT CONSULTANTS
Phone No : 01614145609 , 01884958267

SHEET NO.

S-01

OUTPUT -

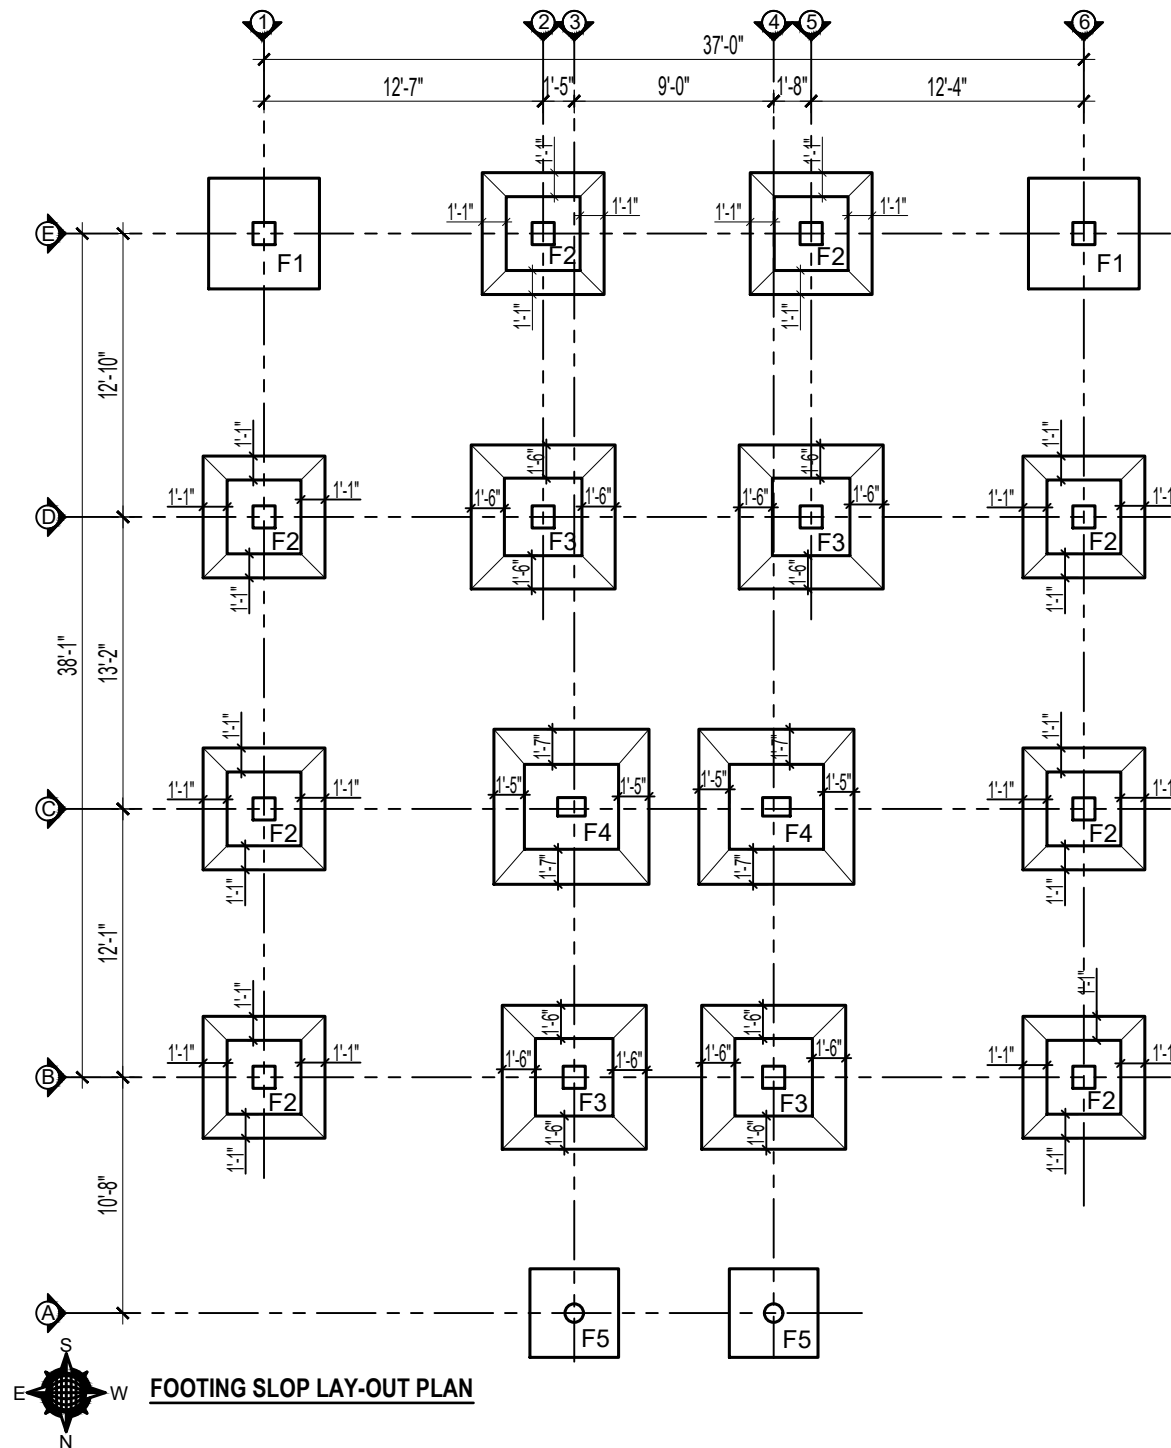

FOOTING SLOP LAY-OUT PLAN

- NOTES -

IN CASE OF ANY CONFUSION IN THE DIMENSIONS OF STRUCTURAL ELEMENT NOT TO SCALE SUCH AS - COLUMN SIZE, BEAM SIZE, SLAB THICKNESS, FALSE SLAB THICKNESS, LINTEL SIZE ETC. THE MEASUREMENT NOT TO SCALE GIVEN IN STRUCTURAL & ARCHITECTURAL DRAWINGS HAS TO BE FOLLOWED.

- PROJECT NAME & ADDRESS -

3- STORIED RESIDENTIAL BUILDING AT CHAR VEDURIYA, BANKERHAT , BHOLA.

- DRAWING TITLE -

FOOTING SLOP LAY-OUT PLAN

ARCHITECT DESIGN / DEVELOPMENT

Architect Md. Aktaruzzaman Khokon
B.Arch (DUET)

Rahima

Diploma Architect

STRUCTURAL DESIGN / DEVELOPMENT

Engr. Md.Hasibul Islam

B.Sc in Civil (IUBAT)

Senior Structure Engr.

Md.Rashed Khan

B.Sc in Civil (PU)

Managing Director

Building planning & Design Engineering

SUPERVISION

Md. Ismail Hossain

Diploma in Civil

Chairman

Building planning & Design Engineering

ELECTRICAL DESIGN / DEVELOPMENT

Md. Masum Patwary

B.Sc in EEE (UIU)

Md. Shamim

Diploma in Electrical

OWNERS NAME

NO.	NAME	SIGNATURE
1.	MD. SHOFIQUE	

Day No:	2332, 1888
KHATIAN NO.	4007
PLOT NO.	
J.AL NO.	056
MOUZA	Char Veduria
TOTAL LAND AREA	3842 Sft



Building Planning & Design Engineering

ENGINEERING SERVICE & MANAGEMENT CONSULTANTS
Phone No : 01614145609 , 01884958267

- SHEET NO. -

S-02


- OUTPUT -

FOOTING SCHEDULE


TYPE OF FOOTING	THICKNESS				SIZE (LxB)	FOOTING STEEL	
	T1	T2	T	K		a	b
F1			12		5'-0" x 5'-0"	(a)16mmØ 6" C/C at Bottom	(b)16mm Ø 6" C/C at Bottom
F2	12	3	15	14	5'-6" x 5'-6"	(a)16mmØ 6" C/C at Bottom	(b)16mm Ø 6" C/C at Bottom
F3	12	3	16	15	6'-6" x 6'-6"	(a)16mmØ 5" C/C at Bottom	(b)16mm Ø 6" C/C at Bottom
F4	14	4	18	18	7'-0" x 7'-0"	(a)16mmØ 5" C/C at Bottom	(b)16mm Ø 5" C/C at Bottom
F5			10		4'-0" x 4'-0"	(a)12mmØ 5" C/C at Bottom	(b)12mm Ø 5" C/C at Bottom

GENERAL INSTRUCTION

1. Reinforcement $F_y = 60G$ (60,000 Psi)
2. Concrete = $F'c = 3,000$ Psi
3. Mixing Ratio of Concrete = 1:1.5:3
4. COARSE AGGREGATES :
3/4" DOWN GRADED BRICK CHIPS TO BE USED
5. CLEAR COVERING = 3" BOTTOM & SIDE

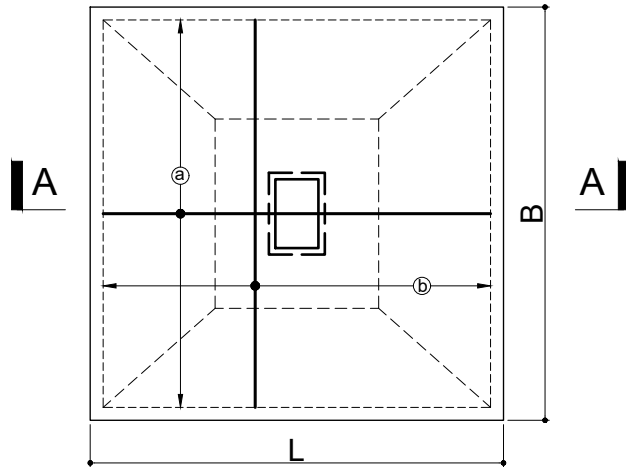

Plan of typical footing

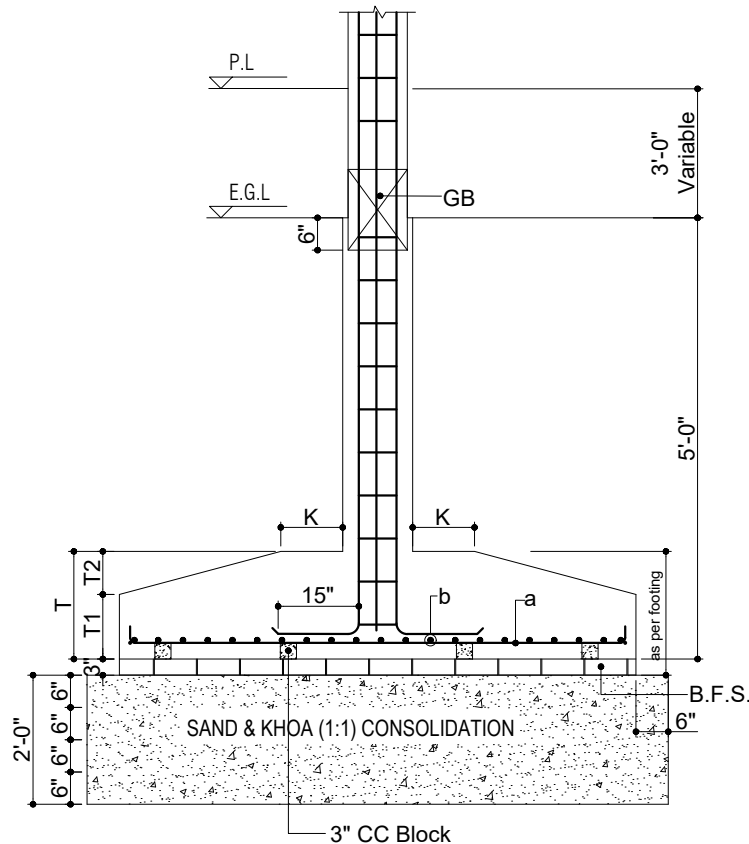

Typical footing section (A-A)

- NOTES -

IN CASE OF ANY CONFUSION IN THE DIMENSIONS OF STRUCTURAL ELEMENT NOT TO SCALE SUCH AS - COLUMN SIZE, BEAM SIZE, SLAB THICKNESS, FALSE SLAB THICKNESS, LINTEL SIZE ETC. THE MEASUREMENT NOT TO SCALE GIVEN IN STRUCTURAL & ARCHITECTURAL DRAWINGS HAS TO BE FOLLOWED.

- PROJECT NAME & ADDRESS -

3- STORIED RESIDENTIAL BUILDING AT CHAR VEDURIYA, BANKERHAT, BHOLA.

- DRAWING TITLE -

REINF. DETAILS OF FOOTING SCHEDULE

ARCHITECT DESIGN / DEVELOPMENT

Architect Md. Aktaruzzaman Khokon
B.Arch (DUET)

Rahima

Diploma Architect

STRUCTURAL DESIGN / DEVELOPMENT

Engr. Md.Hasibul Islam
B.Sc in Civil (IUBAT)
Senior Structure Engr.

Md.Rashed Khan

B.Sc in Civil (PU)
Managing Director
Building planning & Design Engineering

SUPERVISION

Md. Ismail Hossain

Diploma in Civil
Chairman
Building planning & Design Engineering

ELECTRICAL DESIGN / DEVELOPMENT

Md. Masum Patwary

B.Sc in EEE (UIU)

Md. Shamim

Diploma in Electrical

OWNERS NAME

NO.	NAME	SIGNATURE
1.	MD. SHOFIQUE	

Dag No:	2332, 1888
KHATAN NO.	4007
PLOT NO.	
J.A.L NO.	056
MOUZA	Char Veduria
TOTAL LAND AREA	3842 Sft




Building Planning & Design Engineering
ENGINEERING SERVICE & MANAGEMENT CONSULTANTS
Phone No : 01614145609 , 01884958267

- SHEET NO. -

S-03

- OUTPUT -

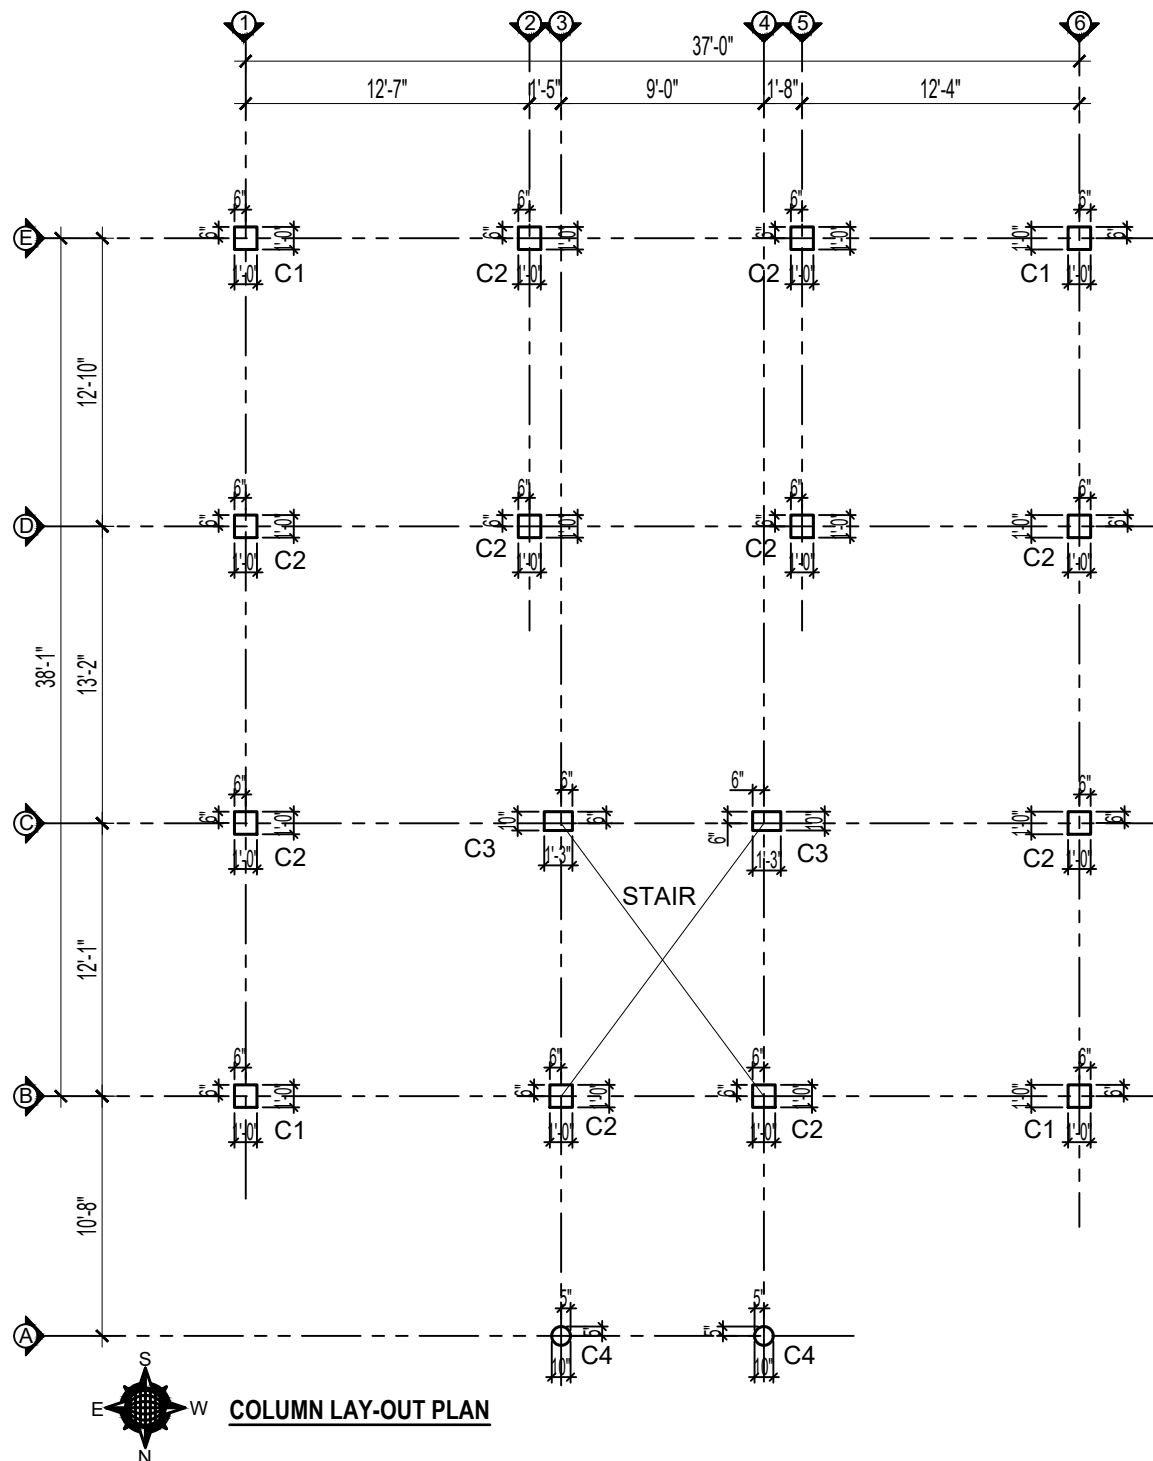

- NOTES -

IN CASE OF ANY CONFUSION IN THE DIMENSIONS OF STRUCTURAL ELEMENT NOT TO SCALE SUCH AS - COLUMN SIZE, BEAM SIZE, SLAB THICKNESS, FALSE SLAB THICKNESS, LINTEL SIZE ETC. THE MEASUREMENT NOT TO SCALE GIVEN IN STRUCTURAL & ARCHITECTURAL DRAWINGS HAS TO BE FOLLOWED.

- PROJECT NAME & ADDRESS -

3- STORIED RESIDENTIAL
BUILDING AT CHAR VEDURIYA,
BANKERHAT , BHOLA.

- DRAWING TITLE -

COLUMN LAY-OUT PLAN

ARCHITECT DESIGN / DEVELOPMENT

Architect Md. Aktaruzzaman Khokon
B.Arch (DUET)

Rahima
Diploma Architect

STRUCTURAL DESIGN / DEVELOPMENT

Engr. Md.Hasibul Islam
B.Sc in Civil (UBAT)
Senior Structure Engr.

Md.Rashed Khan
B.Sc in Civil (PU)
Managing Director
Building planning & Design Engineering

SUPERVISION

Md. Ismail Hossain
Diploma in Civil
Chairmen
Building planning & Design Engineering

ELECTRICAL DESIGN / DEVELOPMENT

Md. Masum Patwary
B.Sc in EEE (UIU)

Md. Shamim
Diploma in Electrical

OWNERS NAME

NO.	NAME	SIGNATURE
1.	MD. SHOFIQUE	

Dag No:	2332, 1888
KHATAN NO.	4007
PLOT NO.	
J.A.L NO.	056
MOUZA	Char Veduria
TOTAL LAND AREA	3842 Sft










**Building Planning &
Design Engineering**
ENGINEERING SERVICE & MANAGEMENT CONSULTANTS
Phone No : 01614145609 , 01884958267

- SHEET NO. -

S-04

- OUTPUT -


COLUMN SCHEDULE

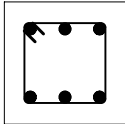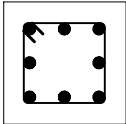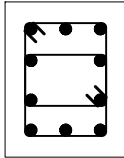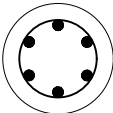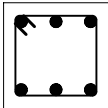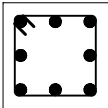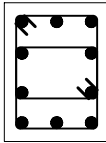FLOOR MARK	C1	C2	C3	C4
BELOW E.G.L	14"x14"  6-16mm Ø	14"x14"  8-16mm Ø	14"x17"  10-16mm Ø	Ø13"  6-12mm Ø
ABOVE E.G.L TO 2ND FLOOR	12"x12"  6-16mm Ø	12"x12"  8-16mm Ø	10"x15"  10-16mm Ø	Ø10"  6-12mm Ø

GENERAL INSTRUCTION

1. Reinforcement $F_y = 60G$ (60,000 Psi)
2. Concrete= $F'_c = 3,000$ Psi
3. Mixing Ratio of Concrete= 1:1.5:3
4. COARSE AGGREGATES :
3/4" DOWN GRADED BRICK CHIPS TO BE USED
5. CLEAR COVERING (Min) = 1.5"

- NOTES -		
IN CASE OF ANY CONFUSION IN THE DIMENSIONS OF STRUCTURAL ELEMENT NOT TO SCALE SUCH AS - COLUMN SIZE, BEAM SIZE, SLAB THICKNESS, FALSE SLAB THICKNESS, LINTEL SIZE ETC. THE MEASUREMENT NOT TO SCALE GIVEN IN STRUCTURAL & ARCHITECTURAL DRAWINGS HAS TO BE FOLLOWED.		
- PROJECT NAME & ADDRESS -		
3- STORIED RESIDENTIAL BUILDING AT CHAR VEDURIYA, BANKERHAT, BHOLA.		
- DRAWING TITLE -		
COLUMN SCHEDULE		
ARCHITECT DESIGN / DEVELOPMENT		
Architect Md. Aktaruzzaman Khokon B.Arch (DUET)		
Rahima Diploma Architect		
STRUCTURAL DESIGN / DEVELOPMENT		
Engr. Md.Hasibul Islam B.Sc in Civil (IUBAT) Senior Structure Engr.		
Md.Rashed Khan B.Sc in Civil (PU) Managing Director Building planning & Design Engineering		
SUPERVISION		
Md. Ismail Hossain Diploma in Civil Chairman Building planning & Design Engineering		
ELECTRICAL DESIGN / DEVELOPMENT		
Md. Masum Patwary B.Sc in EEE (UIU)		
Md. Shamim Diploma in Electrical		
OWNERS NAME		
NO.	NAME	SIGNATURE
1.	MD. SHOFIQUE	
Dag No:		2332, 1888
KHATAN NO.		4007
PLOT NO.		
J.A.L NO.		056
MOUZA		Char Vedia
TOTAL LAND AREA		3842 Sft
 Building Planning & Design Engineering ENGINEERING SERVICE & MANAGEMENT CONSULTANTS Phone No : 01614145609 , 01884958267		
- SHEET NO. -		
S-05		
- OUTPUT -		

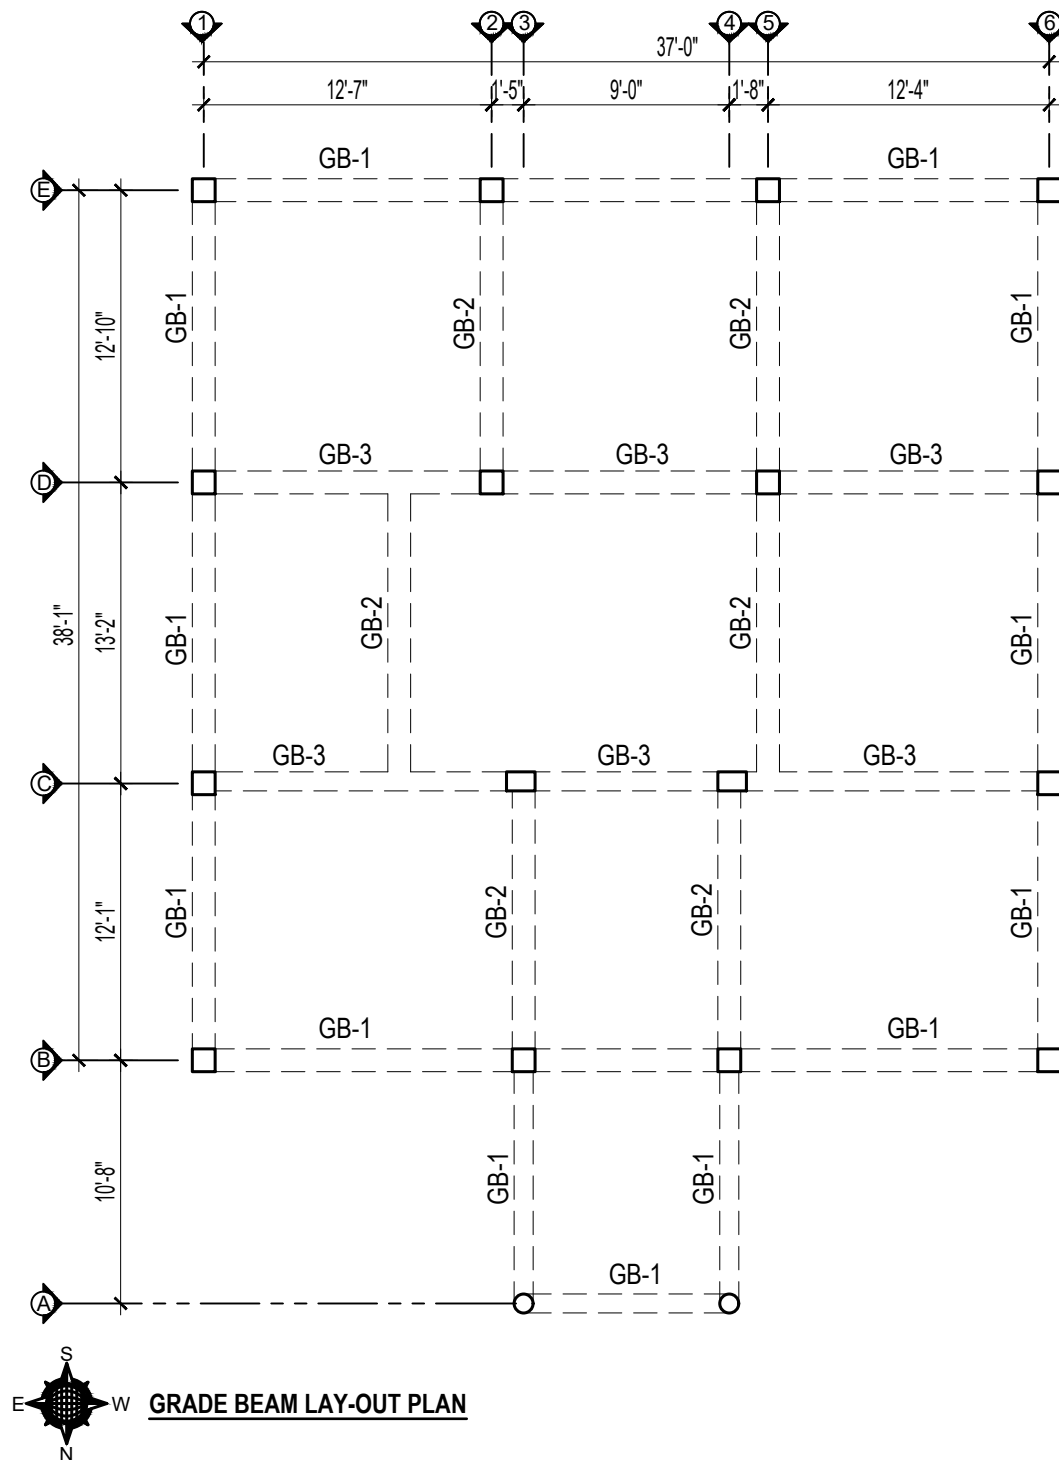

GRADE BEAM LAY-OUT PLAN

- NOTES -

IN CASE OF ANY CONFUSION IN THE DIMENSIONS OF STRUCTURAL ELEMENT NOT TO SCALE SUCH AS - COLUMN SIZE, BEAM SIZE, SLAB THICKNESS, FALSE SLAB THICKNESS, LINTEL SIZE ETC. THE MEASUREMENT NOT TO SCALE GIVEN IN STRUCTURAL & ARCHITECTURAL DRAWINGS HAS TO BE FOLLOWED.

- PROJECT NAME & ADDRESS -

3- STORIED RESIDENTIAL BUILDING AT CHAR VEDURIYA, BANKERHAT , BHOLA.

- DRAWING TITLE -

GRADE BEAM LAY-OUT PLAN

ARCHITECT DESIGN / DEVELOPMENT

Architect Md. Aktaruzzaman Khokon
B.Arch (DUET)

Rahima

Diploma Architect

STRUCTURAL DESIGN / DEVELOPMENT

Engr. Md.Hasibul Islam

B.Sc in Civil (IUBAT)

Senior Structure Engr.

Md.Rashed Khan

B.Sc in Civil (PU)

Managing Director

Building planning & Design Engineering

SUPERVISION

Md. Ismail Hossain

Diploma in Civil

Chairman

Building planning & Design Engineering

ELECTRICAL DESIGN / DEVELOPMENT

Md. Masum Patwary

B.Sc in EEE (UIU)

Md. Shamim

Diploma in Electrical

OWNERS NAME

NO.	NAME	SIGNATURE
1.	MD. SHOFIQUE	

Dag No:	2332, 1888
KHATIAN NO.	4007
PLOT NO.	
J.AL NO.	056
MOUZA	Char Veduria
TOTAL LAND AREA	3842 Sft




Building Planning & Design Engineering

ENGINEERING SERVICE & MANAGEMENT CONSULTANTS
Phone No : 01614145609 , 01884958267


- SHEET NO. -

S-07


- OUTPUT -

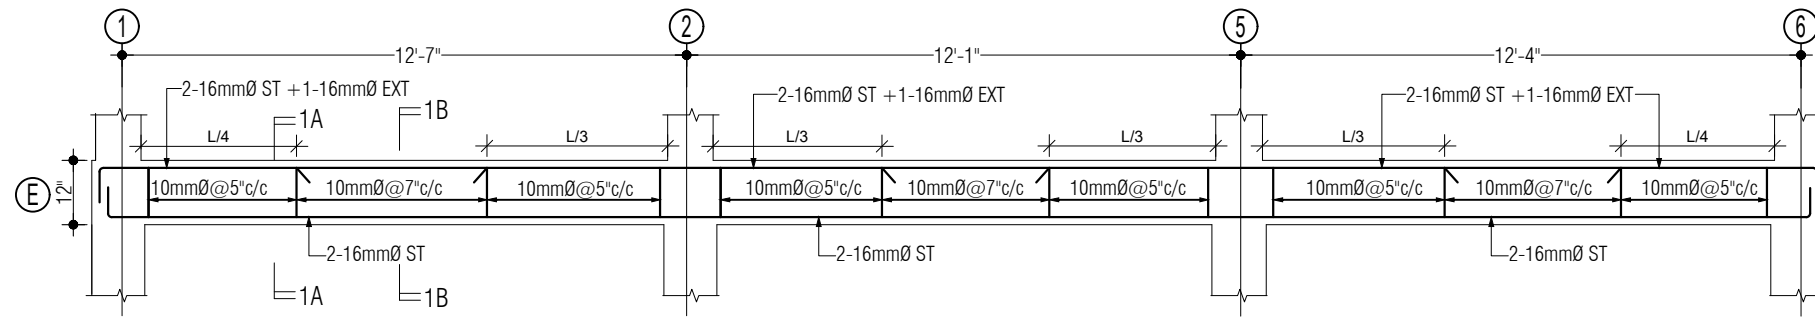


LONG SECTION OF GRADE BEAM GB-1 (12" x 12")

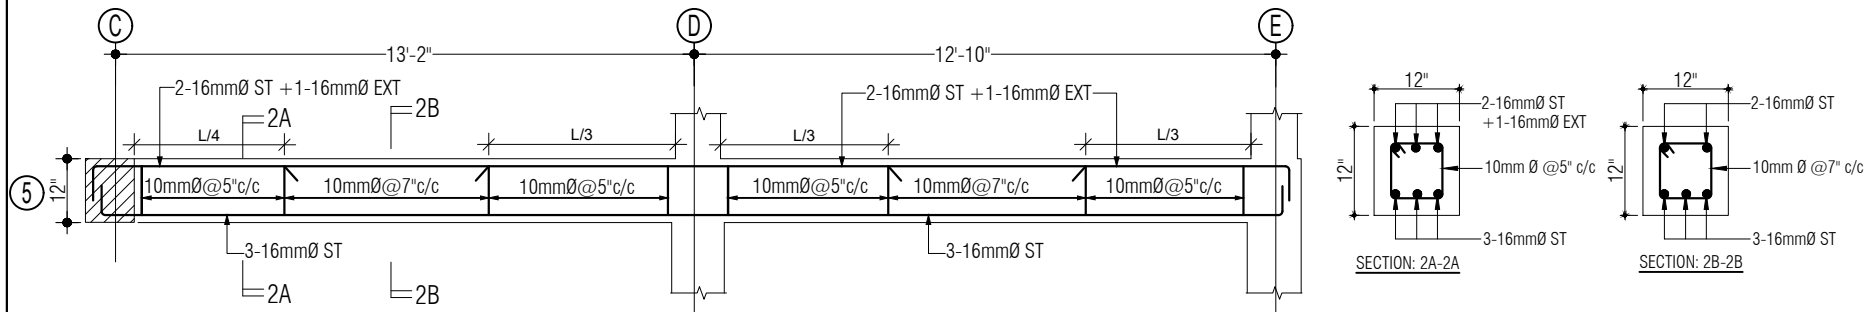

LONG SECTION OF GRADE BEAM GB-2 (12" x 12")

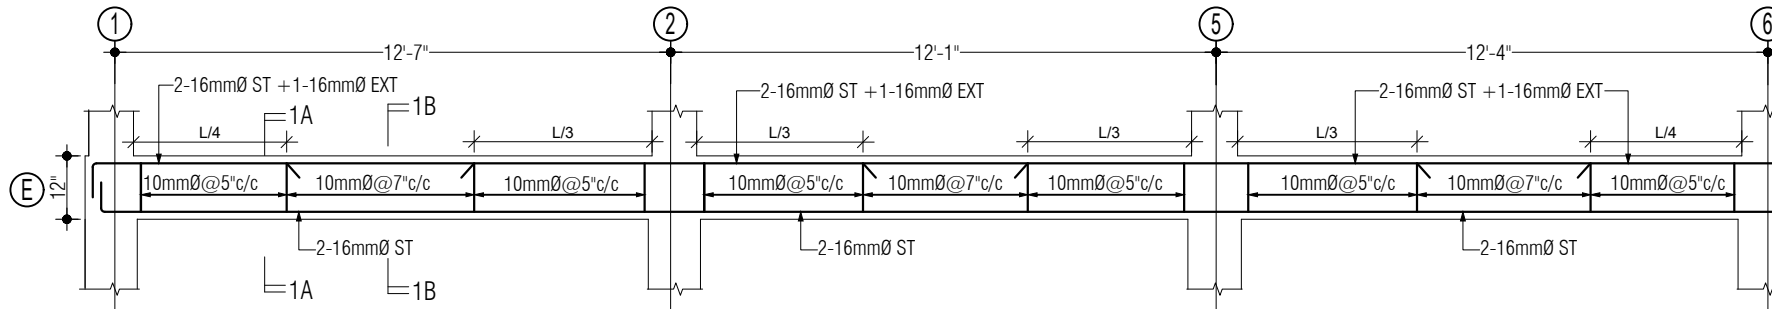


LONG SECTION OF GRADE BEAM GB-1 (12" x 12")

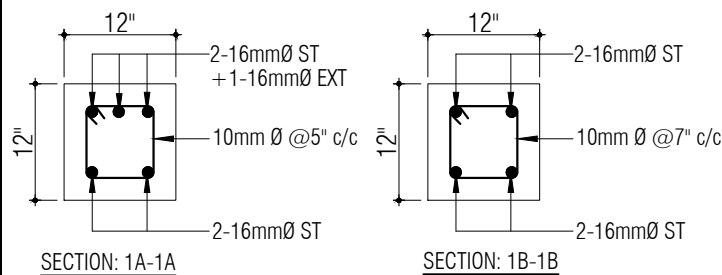

SECTION: 1A-1A

SECTION: 1B-1B

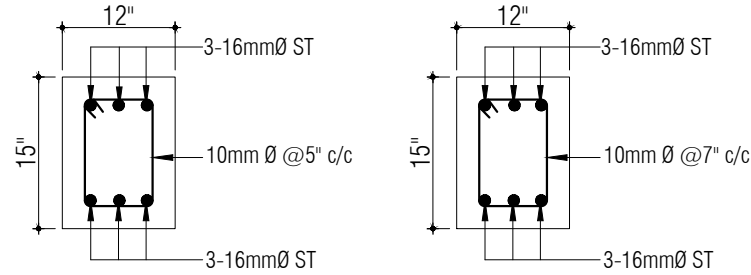

SECTION: 3A-3A

SECTION: 3B-3B

- NOTES -

IN CASE OF ANY CONFUSION IN THE DIMENSIONS OF STRUCTURAL ELEMENT NOT TO SCALE SUCH AS - COLUMN SIZE, BEAM SIZE, SLAB THICKNESS, FALSE SLAB THICKNESS, LINTEL, SIZE ETC. THE MEASUREMENT NOT TO SCALE GIVEN IN STRUCTURAL & ARCHITECTURAL DRAWINGS HAS TO BE FOLLOWED.

- PROJECT NAME & ADDRESS -

3- STORIED RESIDENTIAL BUILDING AT CHAR VEDURIYA, BANKERHAT, BHOLA.

- DRAWING TITLE -

REINF. DETAILS OF GRADE BEAMS

ARCHITECT DESIGN / DEVELOPMENT

Architect Md. Aktaruzzaman Khokon
B.Arch (DUET)

Rahima

Diploma Architect

STRUCTURAL DESIGN / DEVELOPMENT

Engr. Md.Hasibul Islam

B.Sc in Civil (IUBAT)

Senior Structure Engr.

Md.Rashed Khan

B.Sc in Civil (PU)

Managing Director

Building planning & Design Engineering

SUPERVISION

Md. Ismail Hossain

Diploma in Civil

Chairman

Building planning & Design Engineering

ELECTRICAL DESIGN / DEVELOPMENT

Md. Masum Patwary

B.Sc in EEE (UIU)

Md. Shamim

Diploma in Electrical

OWNERS NAME

NO.	NAME	SIGNATURE
1.	MD. SHOFIQUE	

Dag No:	2332, 1888
KHATIAN NO.	4007
PLOT NO.	
J.A.L. NO.	056
MOUZA	Char Veduria
TOTAL LAND AREA	3842 Sft



Building Planning & Design Engineering

ENGINEERING SERVICE & MANAGEMENT CONSULTANTS
Phone No : 01614145609 , 01884958267

- SHEET NO. -

S-08

- OUTPUT -